

1 BASEMENT + GROUND + 3
TYPICAL FLOORS + 4TH PART
FLOOR




BLOCK PLAN

SCALE 1: 500

OCCUPANT LOAD, SANITATION AND PARKING CALCULATIONS FOR "COMMERCIAL COMPLEX"													
Floor	Built-Up Area in sq.m.	RERA Carpet Area in sq.m.	Commercial Occupant Load floor area in sq.m. per person	No. of persons floor-wise	No. of Females 50%	No. of Males 50%	1 No. of Water Closets Required for every 15 Females	1 No. of Wash Basins Required for every 25 Females	1 No. of Water Closets Required for every 25 Males	1 No. of Wash Basins Required for every 25 Males	1 No. of Urinals Required for every 25 Males	2 No. of Car Parking Spaces Required for every 100 sq.m.	5 No. of Scooter Parking Space Required for every 100 sq.m.
Ground	2722.94	2098.22	3	699.4	349.7	349.7	23.3	14.0	14.0	14.0	14.0	148.2	444.0
1st	2779.95	1626.80	6	304.5	152.2	152.2	10.1	6.1	6.1	6.1	6.1	148.2	444.0
2nd	0.00	0.00	0	0.0	0.0	0.0	0.0	0.0	0.0	0.0	0.0	148.2	444.0
3rd	3823.38	2418.86	6	403.1	201.6	201.6	13.4	8.1	8.1	8.1	8.1	148.2	444.0
4th	1087.20	1095.95	6	177.7	88.8	88.8	5.9	3.6	3.6	3.6	3.6	148.2	444.0
Total	11013.46	7490.83		1564.7	782.3	782.3	62.8	31.7	31.7	31.7	31.7	118.6	355.7
							No. of Water Closets Proposed for Females	No. of Wash Basins Proposed for Females	No. of Water Closets Proposed for Males	No. of Wash Basins Proposed for Males	No. of Urinals Proposed for Males		
							60.0	36.0	36.0	36.0	40.0		

PARKING STATEMENT		
Particulars	Car Parking Spaces	Scooter Parking Spaces
Total Required	156.8	546.2
Total Proposed	240	80
Net Difference	83.2	466.2
466.2 Scooter Parking Spaces are deficit, which are compensated by 466.2/8 = 78.2 additional car parking spaces, as per UDCPR clause 8.1.1 v		

OCCUPANT LOAD, SANITATION AND PARKING CALCULATIONS FOR "ART GALLERY & COMMUNITY CENTRE"													
Floor	Built-Up Area in sq.m.	RERA Carpet Area in sq.m.	Institutional Occupant Load floor area in sq.m. per person	No. of persons floor-wise	No. of Females 50%	No. of Males 50%	1 No. of Water Closets Required for every 15 Females	1 No. of Wash Basins Required for every 25 Females	1 No. of Water Closets Required for every 25 Males	1 No. of Wash Basins Required for every 25 Males	1 No. of Urinals Required for every 25 Males	1 No. of Car Parking Spaces Required for every 100 sq.m.	5 No. of Scooter Parking Space Required for every 100 sq.m.
Ground	725.57	636.95	7.5	84.9	42.5	42.5	2.9	1.7	1.7	1.7	1.7	47.4	237.2
1st	1023.82	880.49	7.5	117.4	58.7	58.7	3.9	2.3	2.3	2.3	2.3	47.4	237.2
2nd	3823.38	3225.58	7.5	430.1	215.0	215.0	14.3	8.6	8.6	8.6	8.6	47.4	237.2
3rd	0.00	0.00	7.5	0.0	0.0	0.0	0.0	0.0	0.0	0.0	0.0	47.4	237.2
4th	0.00	0.00	7.5	0.0	0.0	0.0	0.0	0.0	0.0	0.0	0.0	47.4	237.2
Total	5572.77	4743.02		632.4	316.2	316.2	21.1	12.6	12.6	12.6	12.6	37.9	189.7
TOTAL BUA OF THE PROJECT - 16586.23 SQ.M							No. of Water Closets Proposed for Females	No. of Wash Basins Proposed for Females	No. of Water Closets Proposed for Males	No. of Wash Basins Proposed for Males	No. of Urinals Proposed for Males		
							21	15	15	15	15		

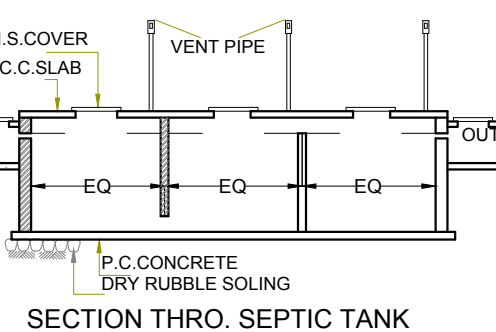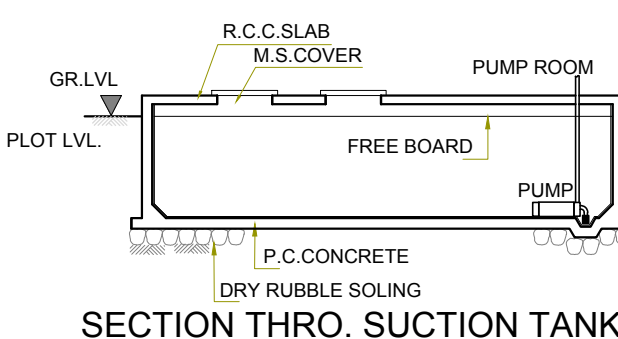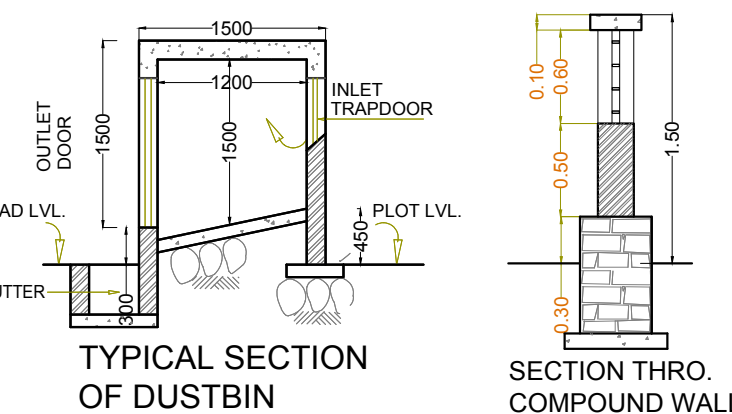

PLOT AREA CALCULATIONS

SCALE 1: 500

BUILT UP AREA CALCULATION										
PLOT AREA CALCULATIONS									SQ.MT.	
AREA UNDER 9 M WIDE ROAD										
1	1/2	X	46.27	X	8.01	X	1	NO	185.31	
2	1/2	X	36.06	X	5.57	X	1	NO	100.43	
TOTAL									285.740	
PLOT AREA										
A	1/2	X	103.93	X	11.87	X	1	NO	616.82	
B	1/2	X	98.56	X	6.50	X	1	NO	323.57	
C	1/2	X	99.12	X	17.43	X	1	NO	863.83	
D	1/2	X	19.33	X	3.67	X	1	NO	35.47	
E	1/2	X	19.33	X	6.61	X	1	NO	63.89	
F	1/2	X	8.03	X	4.09	X	1	NO	16.42	
G	1/2	X	8.03	X	3.50	X	1	NO	14.05	
H	1/2	X	96.14	X	3.84	X	1	NO	184.59	
I	1/2	X	10.60	X	3.12	X	1	NO	16.54	
J	1/2	X	12.06	X	4.01	X	1	NO	24.18	
K	1/2	X	90.58	X	12.04	X	1	NO	545.29	
L	1/2	X	90.58	X	44.19	X	1	NO	2001.37	
M	1/2	X	48.27	X	1.86	X	1	NO	44.89	
N	1/2	X	27.49	X	4.26	X	1	NO	58.55	
O	1/2	X	22.99	X	3.93	X	1	NO	45.18	
P	1/2	X	18.44	X	3.74	X	1	NO	34.48	
TOTAL									4889.120	
EXISTING TEMPLATE										
a	(	4.24	+	4.04	)	/	2	X	6.54 X 1 NO	27.08
b	(	8.26	+	9.62	)	/	2	X	6.69 X 1 NO	59.81
TOTAL									86.890	
TOTAL ADDITION									5261.750	

LOCATION PLAN

SCALE 1: 2000



BASEMENT PLAN


SCALE 1: 200

OWNER'S SIGN
FOR KDMC, THE CITY ENGINEERCONCESSIONAIRE'S SIGN
FOR DASHREE DEVELOPERS PVT. LTD.

ARCHITECT'S SIGN




Ar. ATIT MISTRY

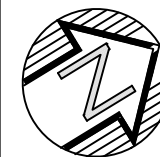ENVIRONMENTAL ARCHITECT + INTERIOR DESIGNER
info.aratimistry@gmail.com
217, SHREE KRISHNA INDUSTRIAL PREMISES CSL, WESTERN
EXPRESS HIGHWAY, DAHISAR EAST, MUMBAI, INDIA 400068

PROFORMA - A				
Sr.No	AREA STATEMENT	AREA IN SQ.MT.		
1)	Plot Area	5262.00		
	(a) As per ownership document (7/12 extract)	5262.00		
	(b) as per measurement sheet	5262.00		
	(c) as per site	5262.00		
	(d) Total Plot area considered for BUA calculations	5262.00		
2)	Deductions for	--		
	(a) 9.00m wide DP road	NIL		
	(b) 24.00m wide DP road	NIL		
	(c) Total Deductions	NIL		
3)	Balance area of plot (1-2)	5262.00		
4)	Amenity Space (if applicable)	--		
	(a) Required (5% x sr. no.3)	NIL		
	(b) Adjustment of 2(d) & 2(e), if any	NIL		
	(c) Balance Proposed	NIL		
5)	Net Plot Area (3-4 c)	5262.00		
6)	Recreational Open space (if applicable)	--		
	(a) Required (10% x sr. no. 3)	NIL		
	(b) Proposed	NIL		
7)	Internal Road area	NIL		
8)	Plotable area (if applicable)	5262.00		
	PARTICULARS	1/3rd AREA FOR "ART GALLERY & COMMUNITY CENTER"	2/3rd AREA FOR COMMERCIAL COMPLEX	TOTAL
9)	Built up area with Basic F.S.I. as per front road width (Sr. No. 5x1.10)	1929.40	3858.80	5788.20
10)	Addition of FSI on payment of premium			--
	(a) Maximum permissible premium FSI - based on road width / TOD Zone, (5x0.50)	877.00	1754.00	2631.00
	(b) Proposed premium FSI	877.00	1754.00	2631.00
11)	In-situ FSI / TDR loading	--	--	--
	(a) In-situ area DP road (2.00x(2a+2b+2c))	NIL	NIL	NIL
	(b) In-situ area against Amenity Space if handed over (2.00 or 1.85 x 4b and / or 4c(b))	NIL	NIL	NIL
	(c) TDR area permissible (5x1.15)	2017.10	4034.20	6051.30
	(d) Total in-situ FSI / TDR loading proposed	289.58	505.79	795.37
12)	Additional FSI area under Chapter No. 7	NIL	NIL	NIL
13)	Total entitlement of FSI in the proposal	--	--	--
	(a) (9 + 10(b)+11(d)) or 12 whichever is applicable.	3095.98	6118.59	9214.57
	(b) Ancillary area up to 60% or 80% with payment of charges	2476.79	4894.87	7371.66
	(c) Total Entitlement (a+b)	5572.77	11013.46	16586.23
14)	Max. utilization of FSI (building potential) as per road width (as per reg. no. 6.1 or 6.2 or 6.3 or 6.4 as applicable) x 1.6 or 1.8	5572.77	11013.46	16586.23
15)	Total Built-up Area in proposal (excluding area at Sr.No.17 b)	--	--	--
	(a) Existing Built-up Area of Mandir	NIL	130.00	130.00
	(b) Proposed Built-up Area (as per P-line)	5572.77	11143.46	16716.23
	(c) total BUA area (a+b)	5572.77	11143.46	16716.23
16)	FSI Consumed (15/5) (shouldnot be more than sr. no. 15)	3.176		
17)	Area for Inclusive Housing, if any			
	(a) Required(20% of Sr.No.5)	NIL		
	(b) Proposed	NIL		
18)	Balance BUA including ancillary area	NIL		
AREA CERTIFICATE	CERTIFIED THAT THE PLOT UNDER REFERENCE WAS SURVEYED BY ME ON 15/03/11. & THE DIMENSIONS OF SIDES ETC. OF PLOT STATED ON PLAN ARE AS MEASURED ON THE SITE & THE AREA SO WORKED OUT TALLIES WITH THE AREA STATED IN THE DOCUMENT OF OWNERSHIP/T.P. SCHEME RECORDS DEPTT./CITY SURVEY RECORDS.			
	ARCHITECT'S SIGN			
PROJECT	PROPOSED FBT/BOT PROJECT OF "ART GALLERY & COMMUNITY CENTER" AND "COMMERCIAL COMPLEX" KNOWN AS "GANESHA GALAXY" ON RESERVATION NO. 27 AT LAL CHOWKY, JUNCTION OF AGRA ROAD AND AADHARWADI ROAD, ON PLOT BEARING S. NO. 1/1 OF VILLAGE KALYAN, TALUKA KALYAN, KALYAN WEST, THANE - 421301. PREVIOUS APPROVAL NO.: KDMC/NRV/BP/KV/2013-14/182 DATED:24/2/2014 KALYAN DOMBIVLI MUNICIPAL CORPORATION			

STAMP AND DATE OF APPROVAL

2

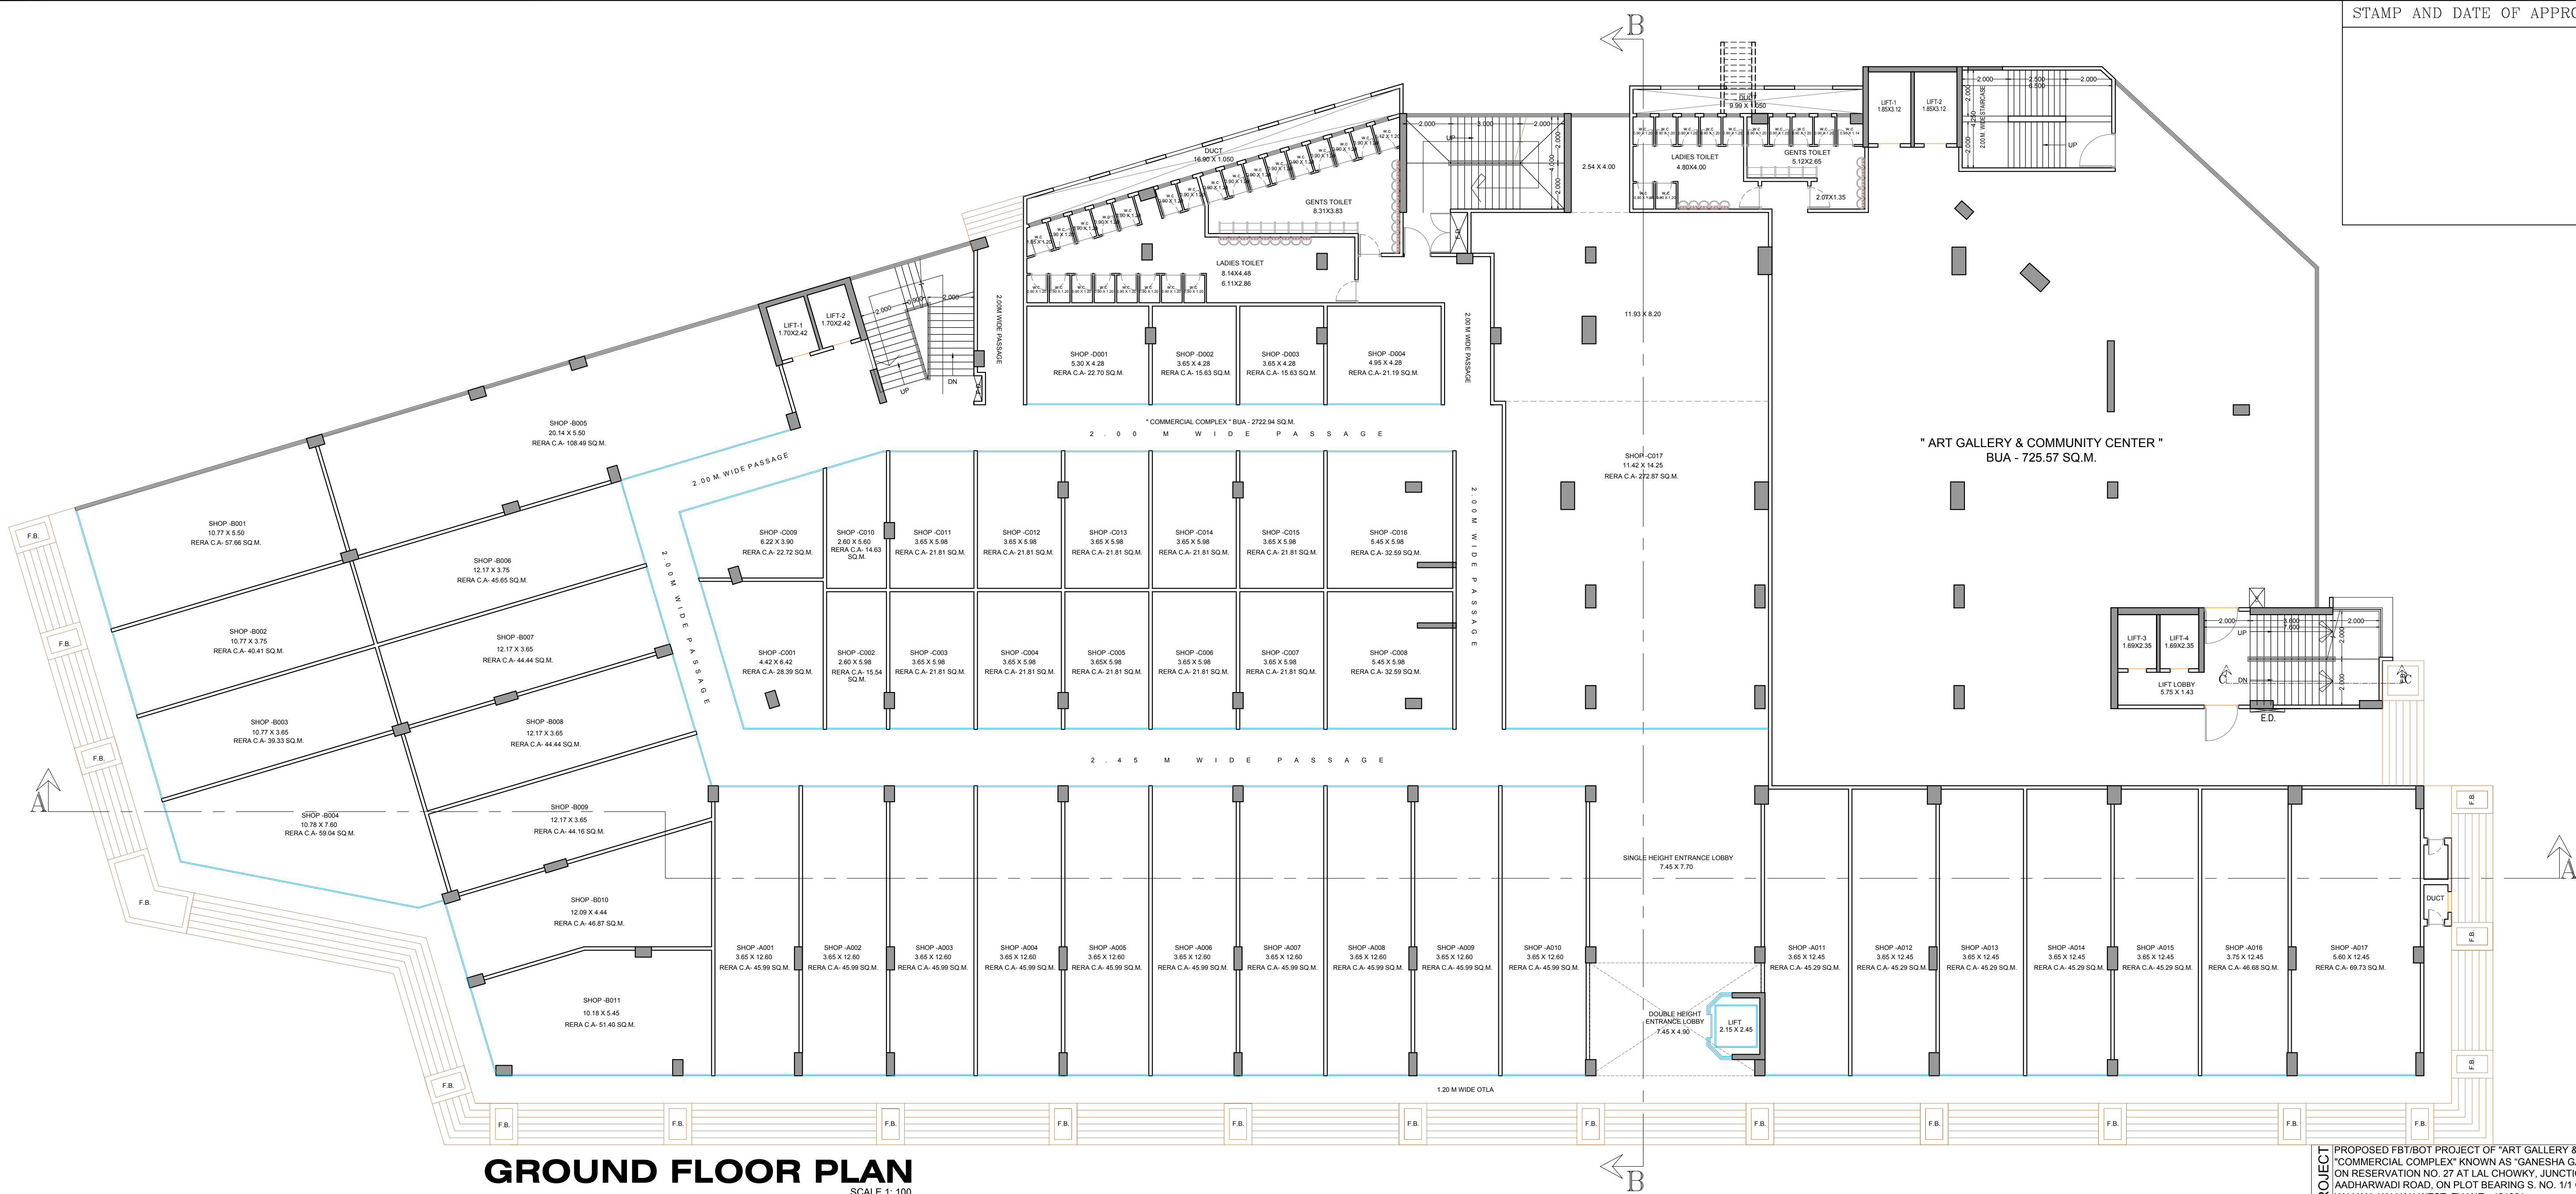

GROUND FLOOR PLAN
SCALE 1: 100

PROPOSED FBT/BOT PROJECT OF "ART GALLERY & COMMUNITY CENTER" AND "COMMERCIAL COMPLEX" KNOWN AS "GANESHA GALAXY" ON RESERVATION NO. 27 AT LAL CHOWKY, JUNCTION OF AGRA ROAD AND AADHARWADI ROAD, ON PLOT BEARING S. NO. 1/11 OF VILLAGE KALYAN, TALUKA KALYAN, KALYAN WEST, THANE - 421301
PREVIOUS APPROVAL NO. KDMC/NR/BJ/KV/2013-14/182 DATED 24/2/2014
KALYAN DOMBIVLI MUNICIPAL CORPORATION

ARCHITECT


AR. ATIT MISTRY
ENVIRONMENTAL ARCHITECT + INTERIOR DESIGNER
info.aratimistry@gmail.com

217, SHREE KRISHNA INDUSTRIAL PREMISES CSL, WESTERN EXPRESS HIGHWAY, DAHISAR EAST, MUMBAI, INDIA 400068

OWNER'S SIGN
FOR KDMC, THE CITY ENGINEER

CONCESSIONAIRE'S SIGN
FOR DHANSHREE DEVELOPERS PVT. LTD.

ARCHITECT'S SIGN

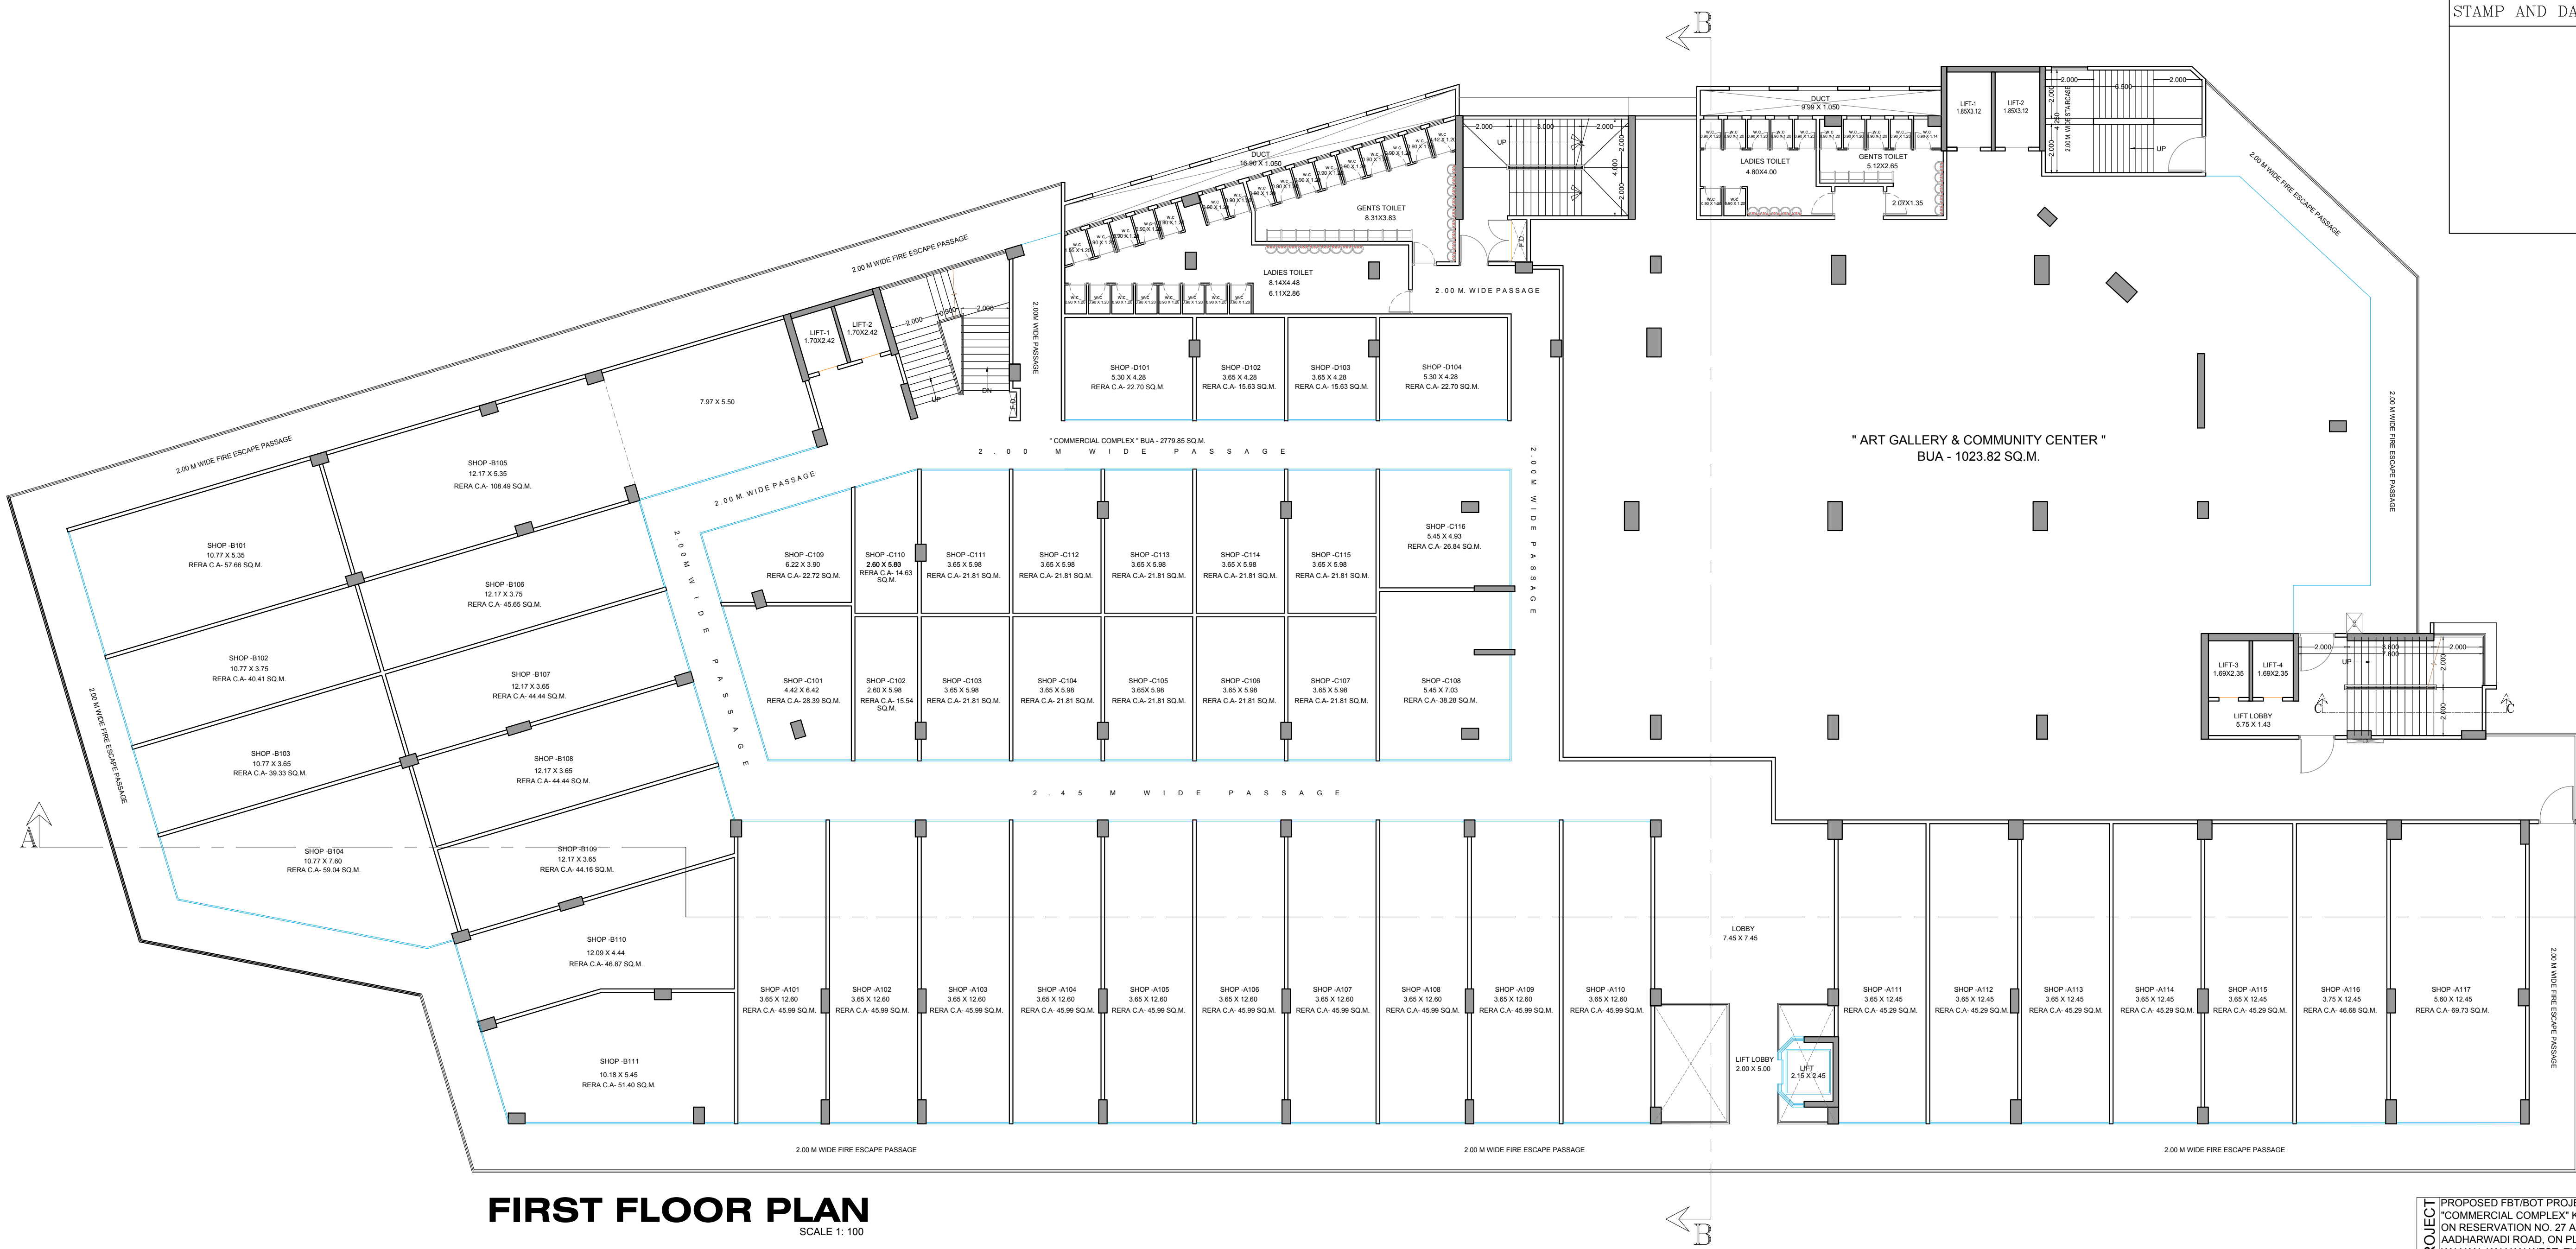


PROPOSED FBT/BOT PROJECT OF "ART GALLERY & COMMUNITY CENTER" AND "COMMERCIAL COMPLEX" KNOWN AS "GANESHA GALAXY" ON RESERVATION NO. 27 AT LAL CHOWKY, JUNCTION OF AGRA ROAD AND AADHARWADI ROAD, ON PLOT BEARING S. NO. 1/1 OF VILLAGE KALYAN, TALUKA KALYAN, KALYAN WEST, THANE - 421301. PREVIOUS APPROVAL NO. KDMC/NR/BI/KV/2013-14/182 DATED 24/2/2014. KALYAN DOMBIVLI MUNICIPAL CORPORATION.

ARCHITECT



Ar. ATIT MISTRY


ENVIRONMENTAL ARCHITECT + INTERIOR DESIGNER
info.aratimistry@gmail.com
217, SHREE KRISHNA INDUSTRIAL PREMISES CSL, WESTERN EXPRESS HIGHWAY, DAHSAR EAST, MUMBAI, INDIA 400068

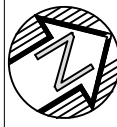

OWNER'S SIGN
FOR KDMC, THE CITY ENGINEER

CONCESSIONAIRE'S SIGN
FOR DHANSHREE DEVELOPERS PVT. LTD.

ARCHITECT'S SIGN

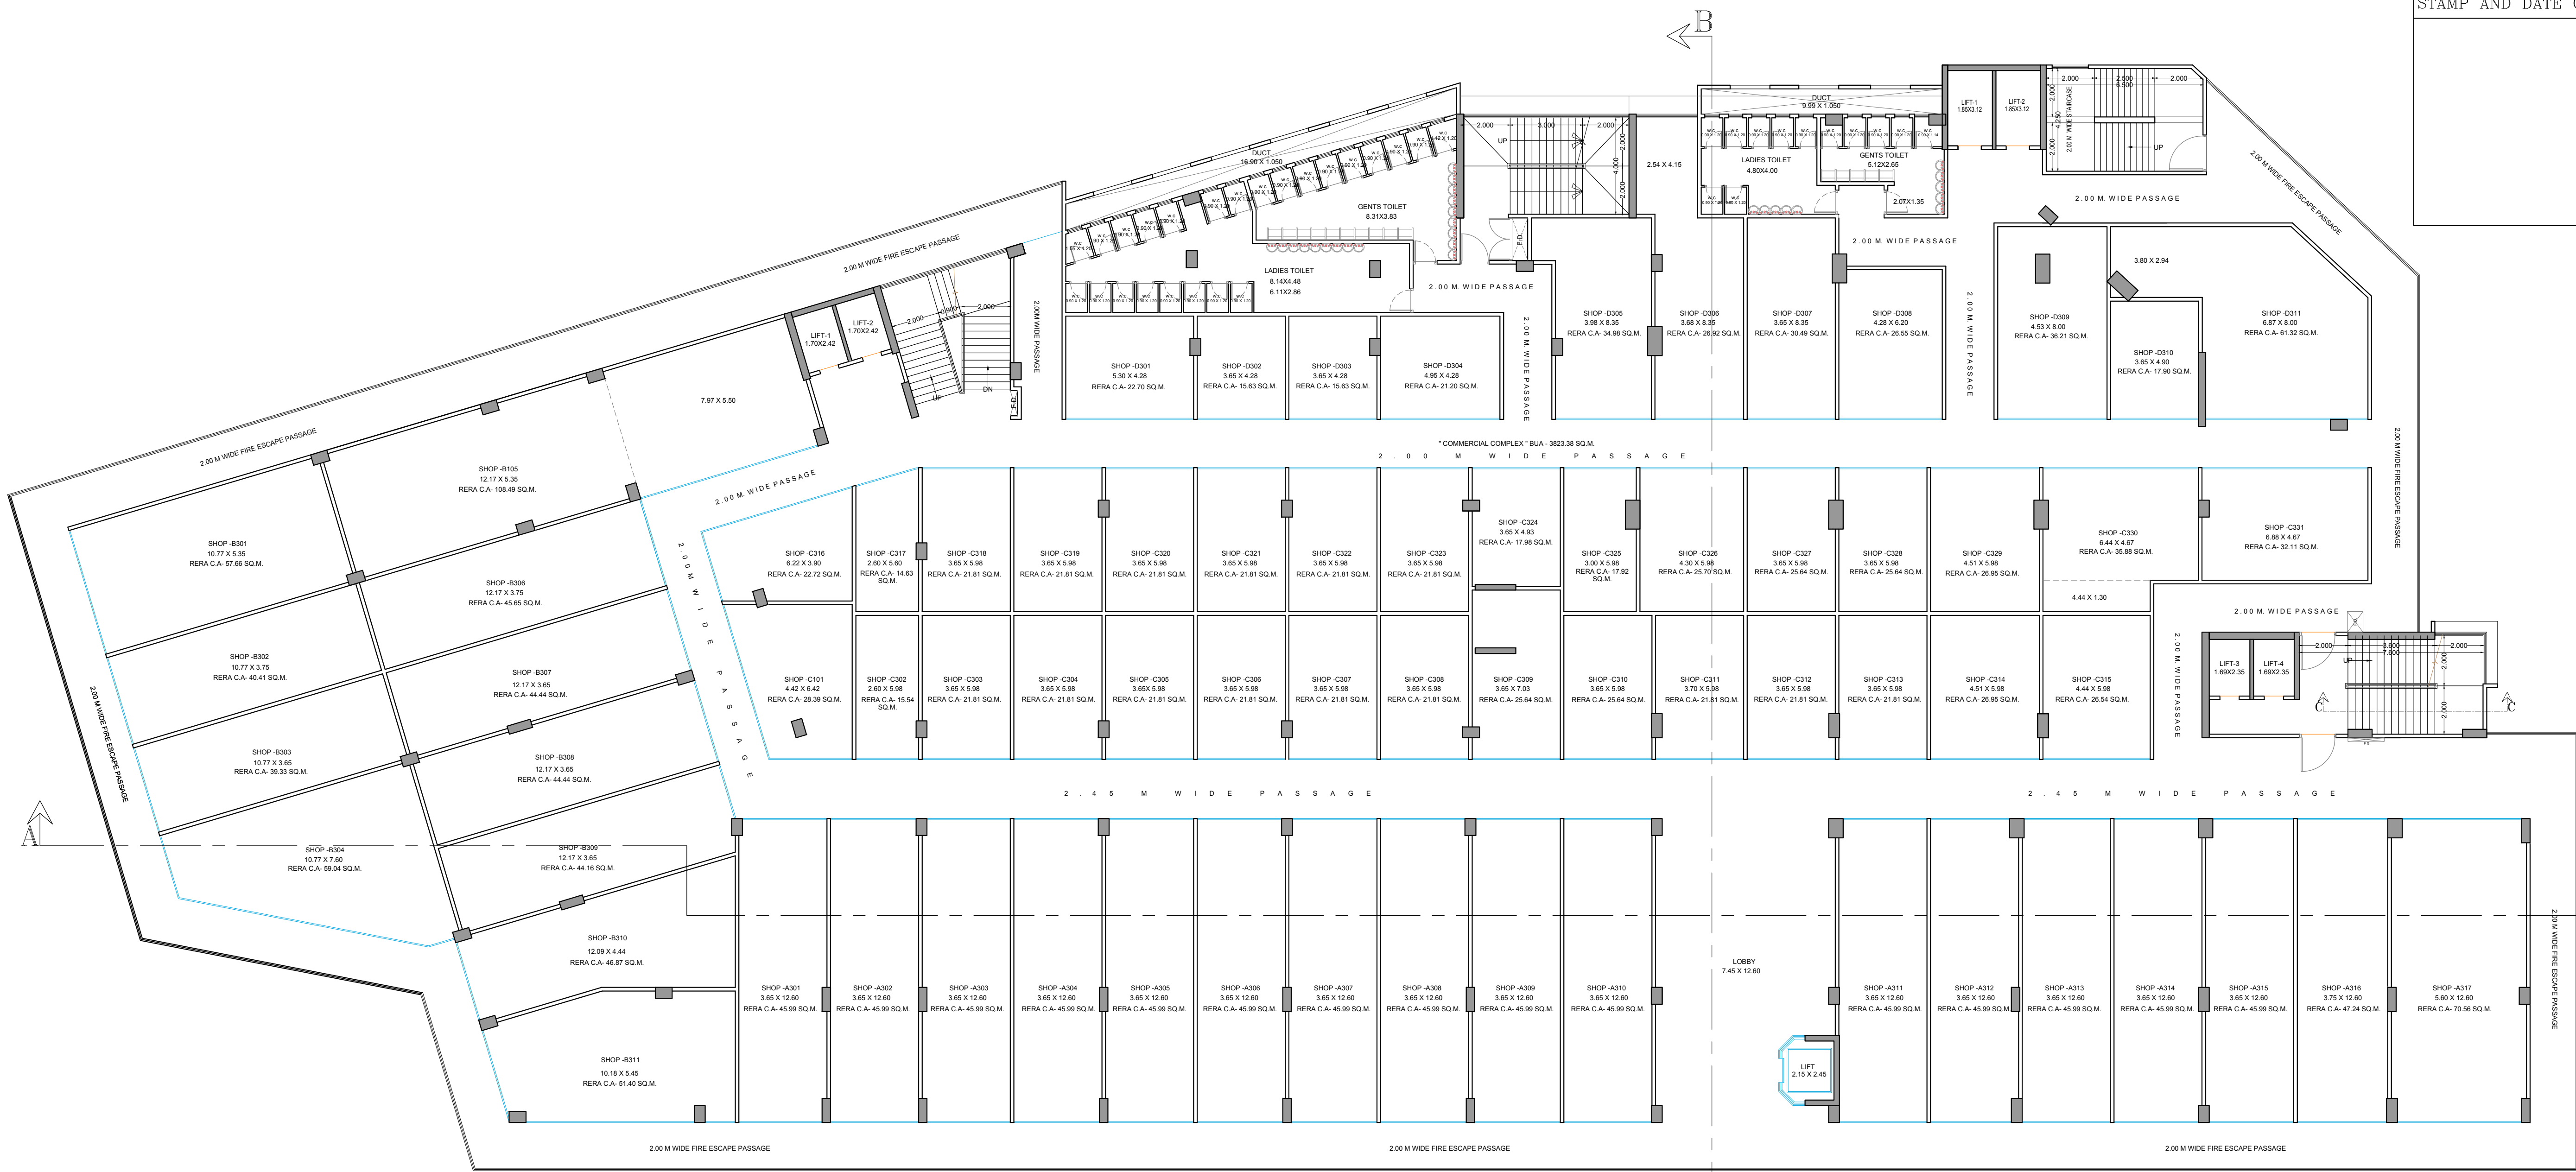

THIRD FLOOR PLAN

SCALE 1: 100

PROPOSED FBT/BOT PROJECT OF "ART GALLERY & COMMUNITY CENTER" AND "COMMERCIAL COMPLEX" KNOWN AS "GANESHA GALAXY" ON RESERVATION NO. 27 AT LAL CHOWKY, JUNCTION OF AGRA ROAD AND AADHARWADI ROAD, ON PLOT BEARING S. NO. 1/1 OF VILLAGE KALYAN, TALUKA KALYAN, KALYAN WEST, THANE - 421301. PREVIOUS APPROVAL NO. KDMC/NR/BPK/2013-14/182 DATED 24/2/2014 KALYAN DOMBIVLI MUNICIPAL CORPORATION






ARCHITECT

Ar. Atit Mistry
ENVIRONMENTAL ARCHITECT + INTERIOR DESIGNER
info.aratimistry@gmail.com
217, SHREE KRISHNA INDUSTRIAL PREMISES CSL, WESTERN EXPRESS HIGHWAY, DAHISAR EAST, MUMBAI, INDIA 400068

OWNER'S SIGN
FOR KDMC, THE CITY ENGINEER

CONCESSIONAIRE'S SIGN
FOR DHANSHREE DEVELOPERS PVT. LTD.

ARCHITECT'S SIGN

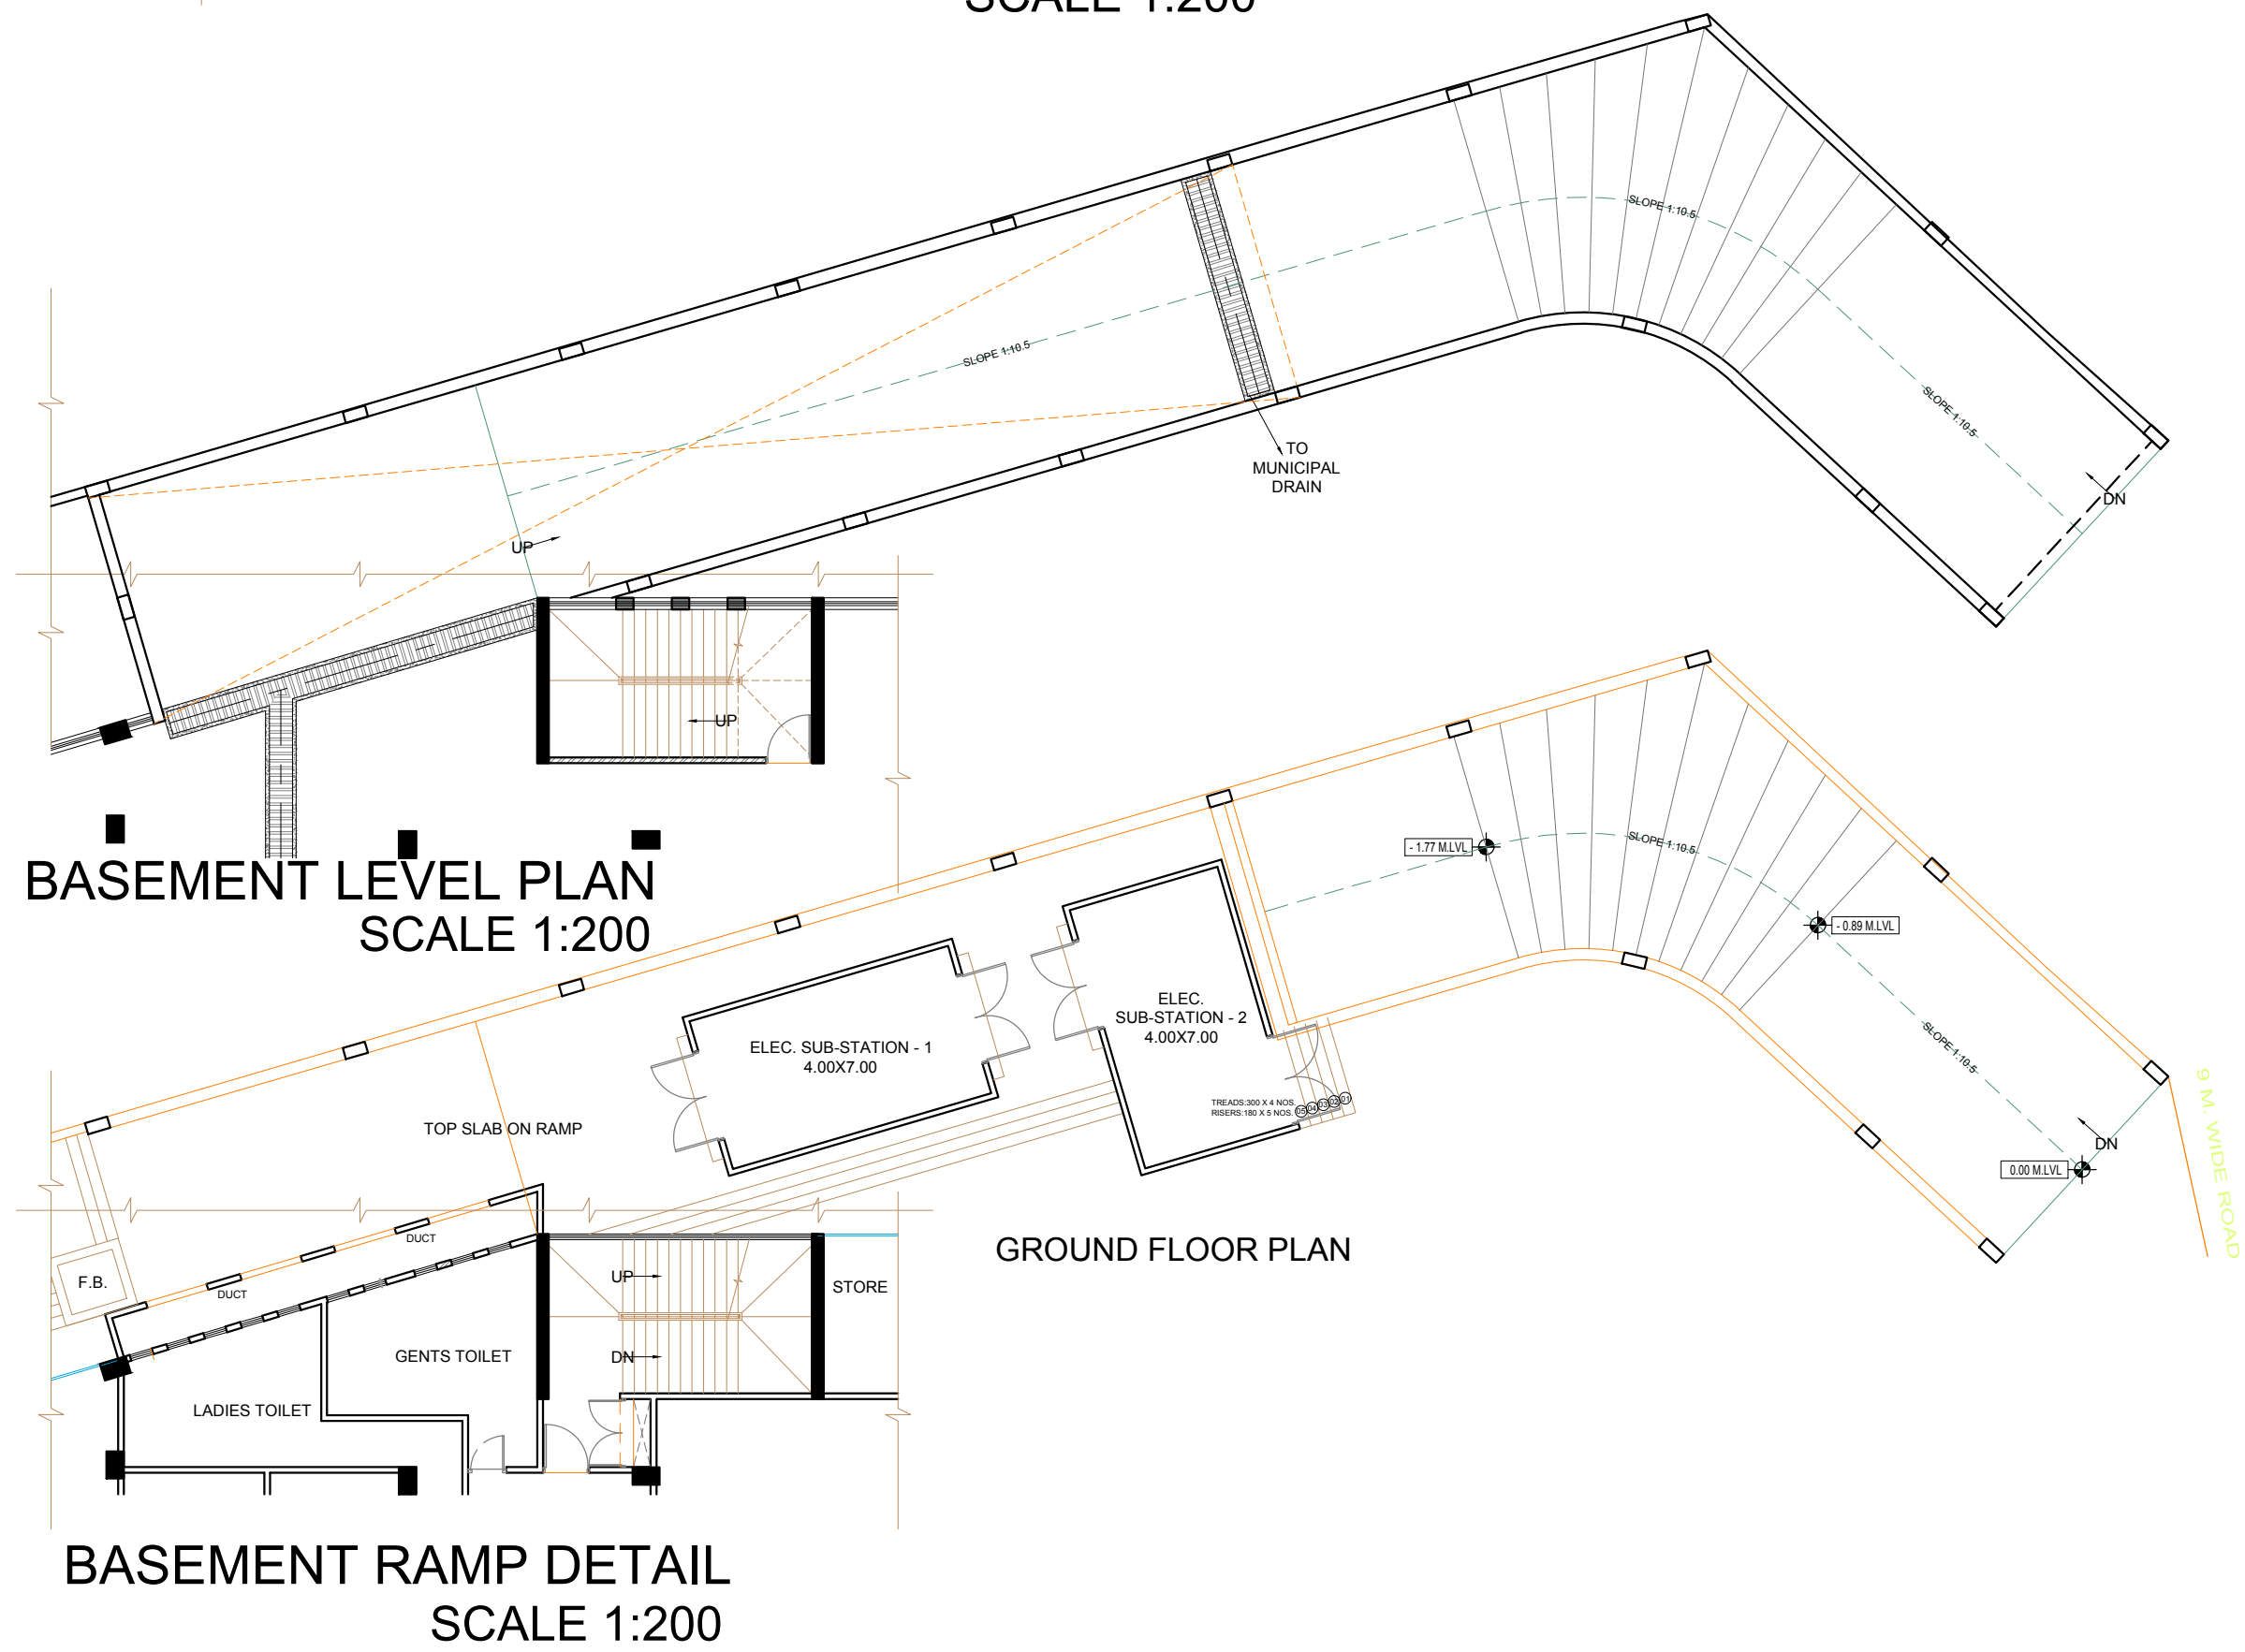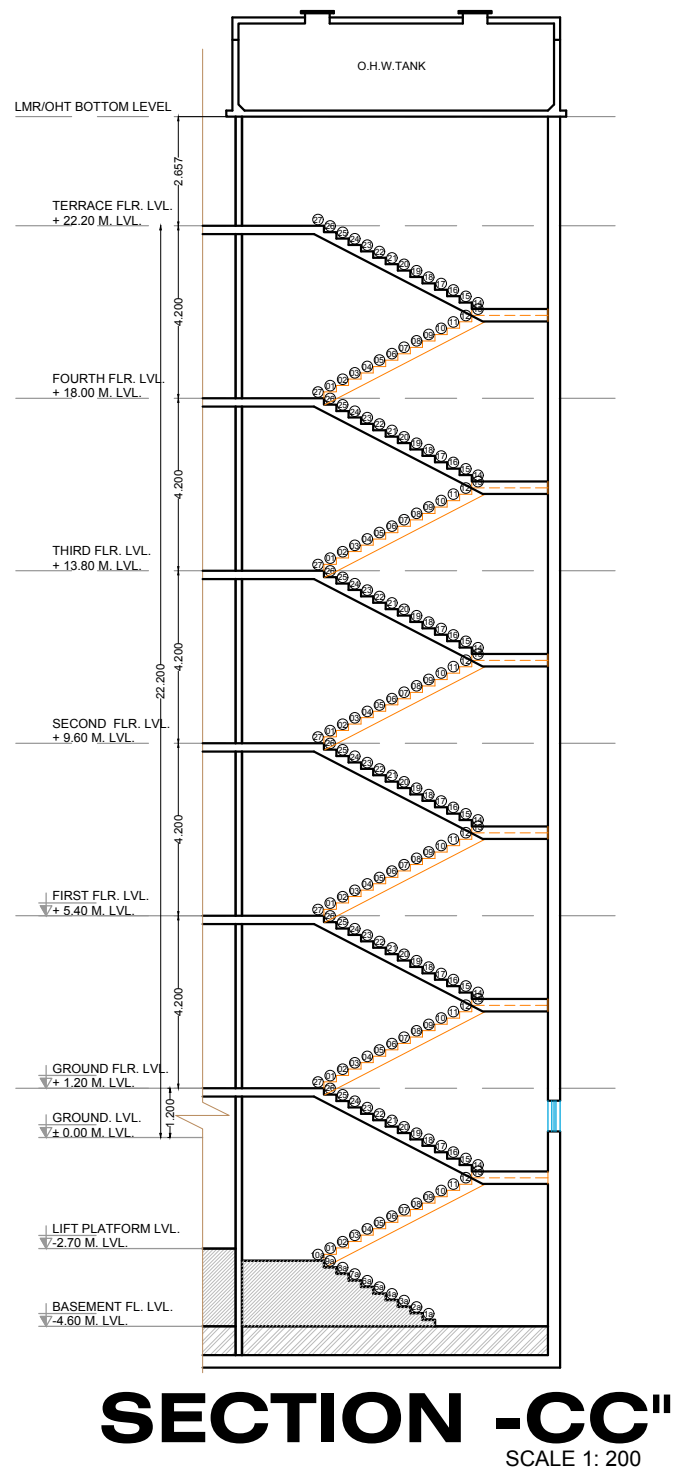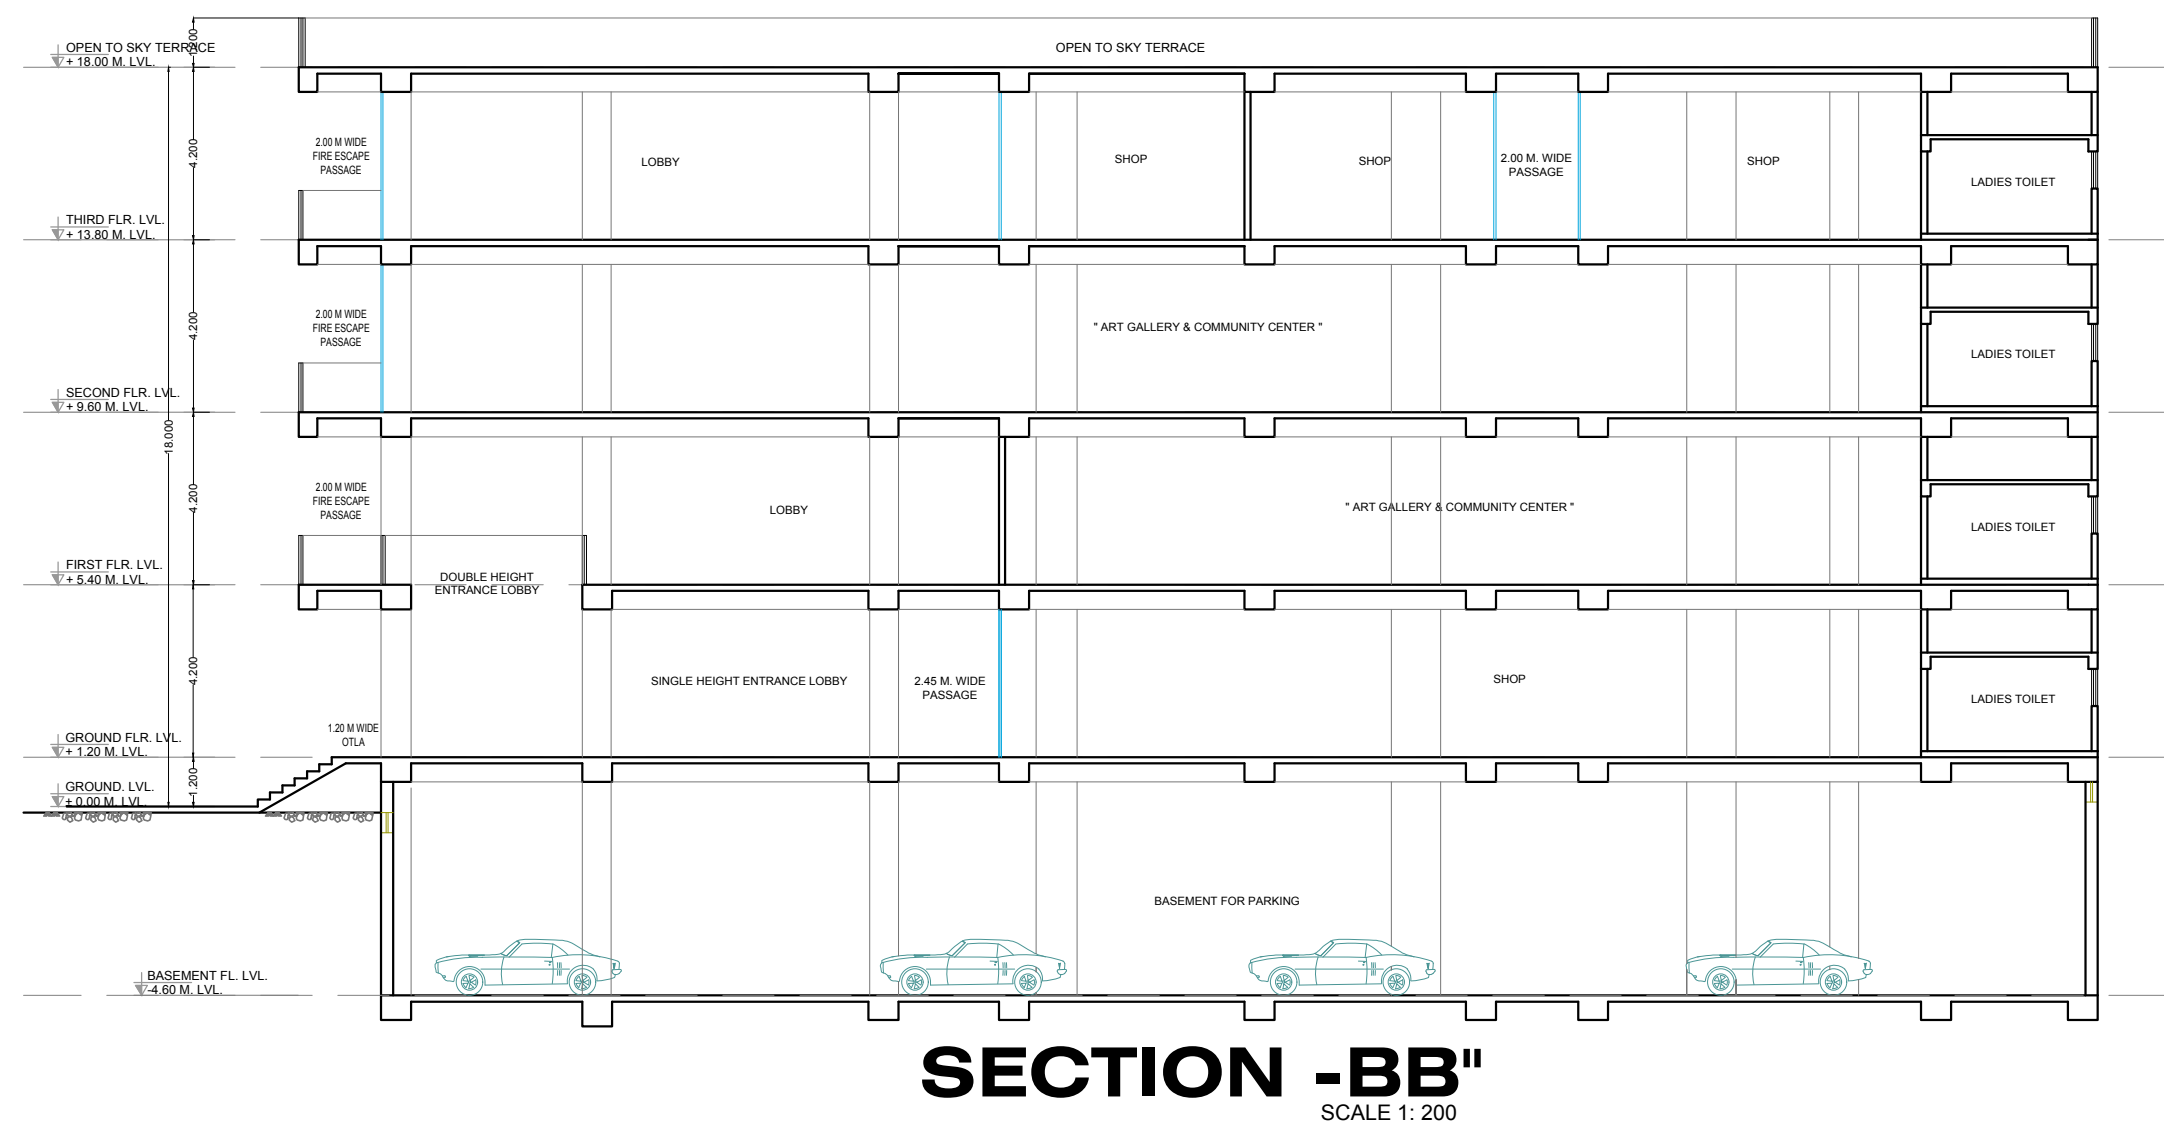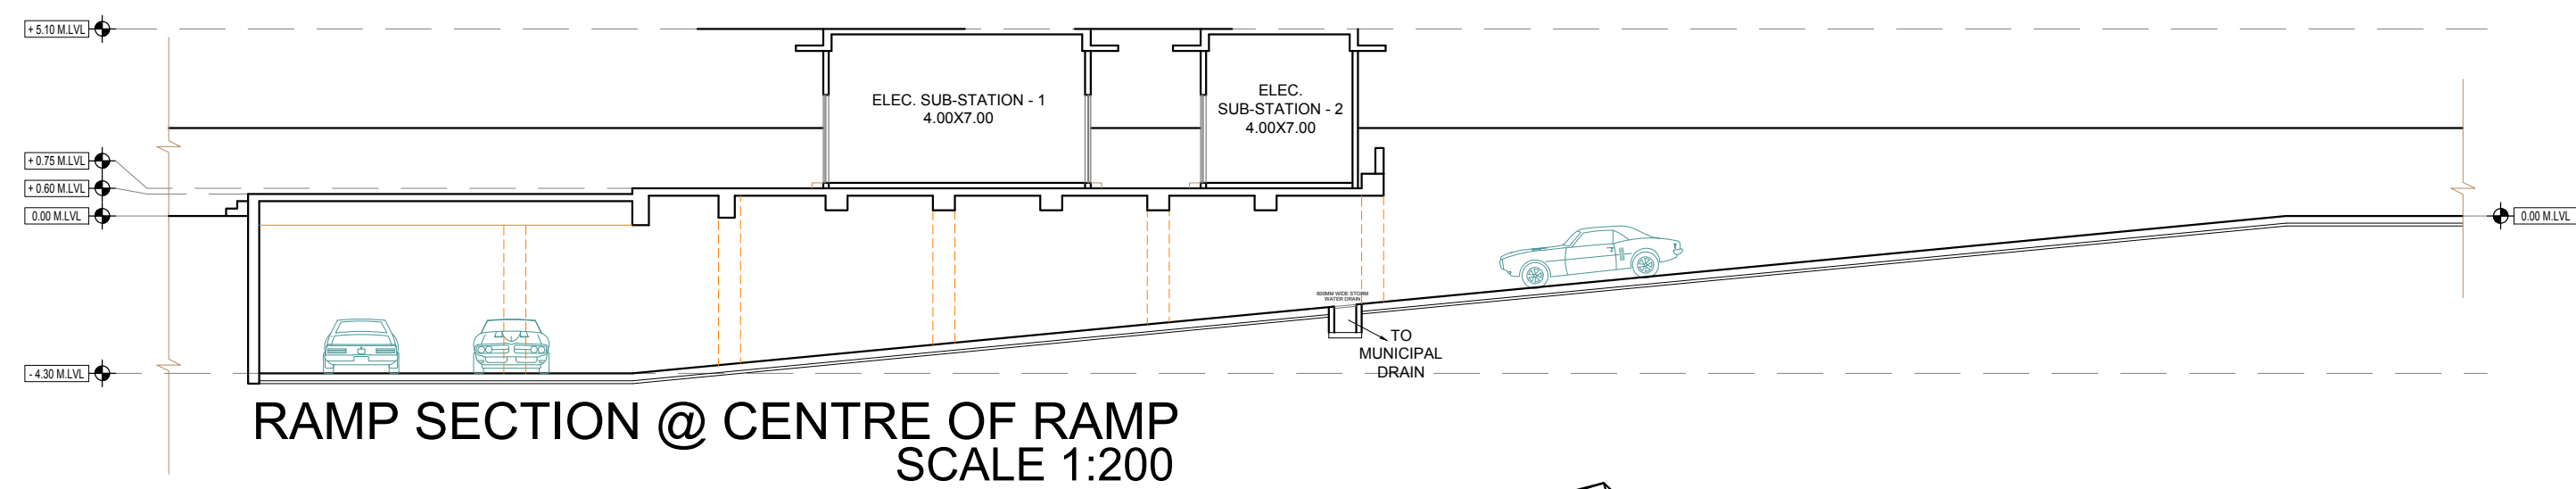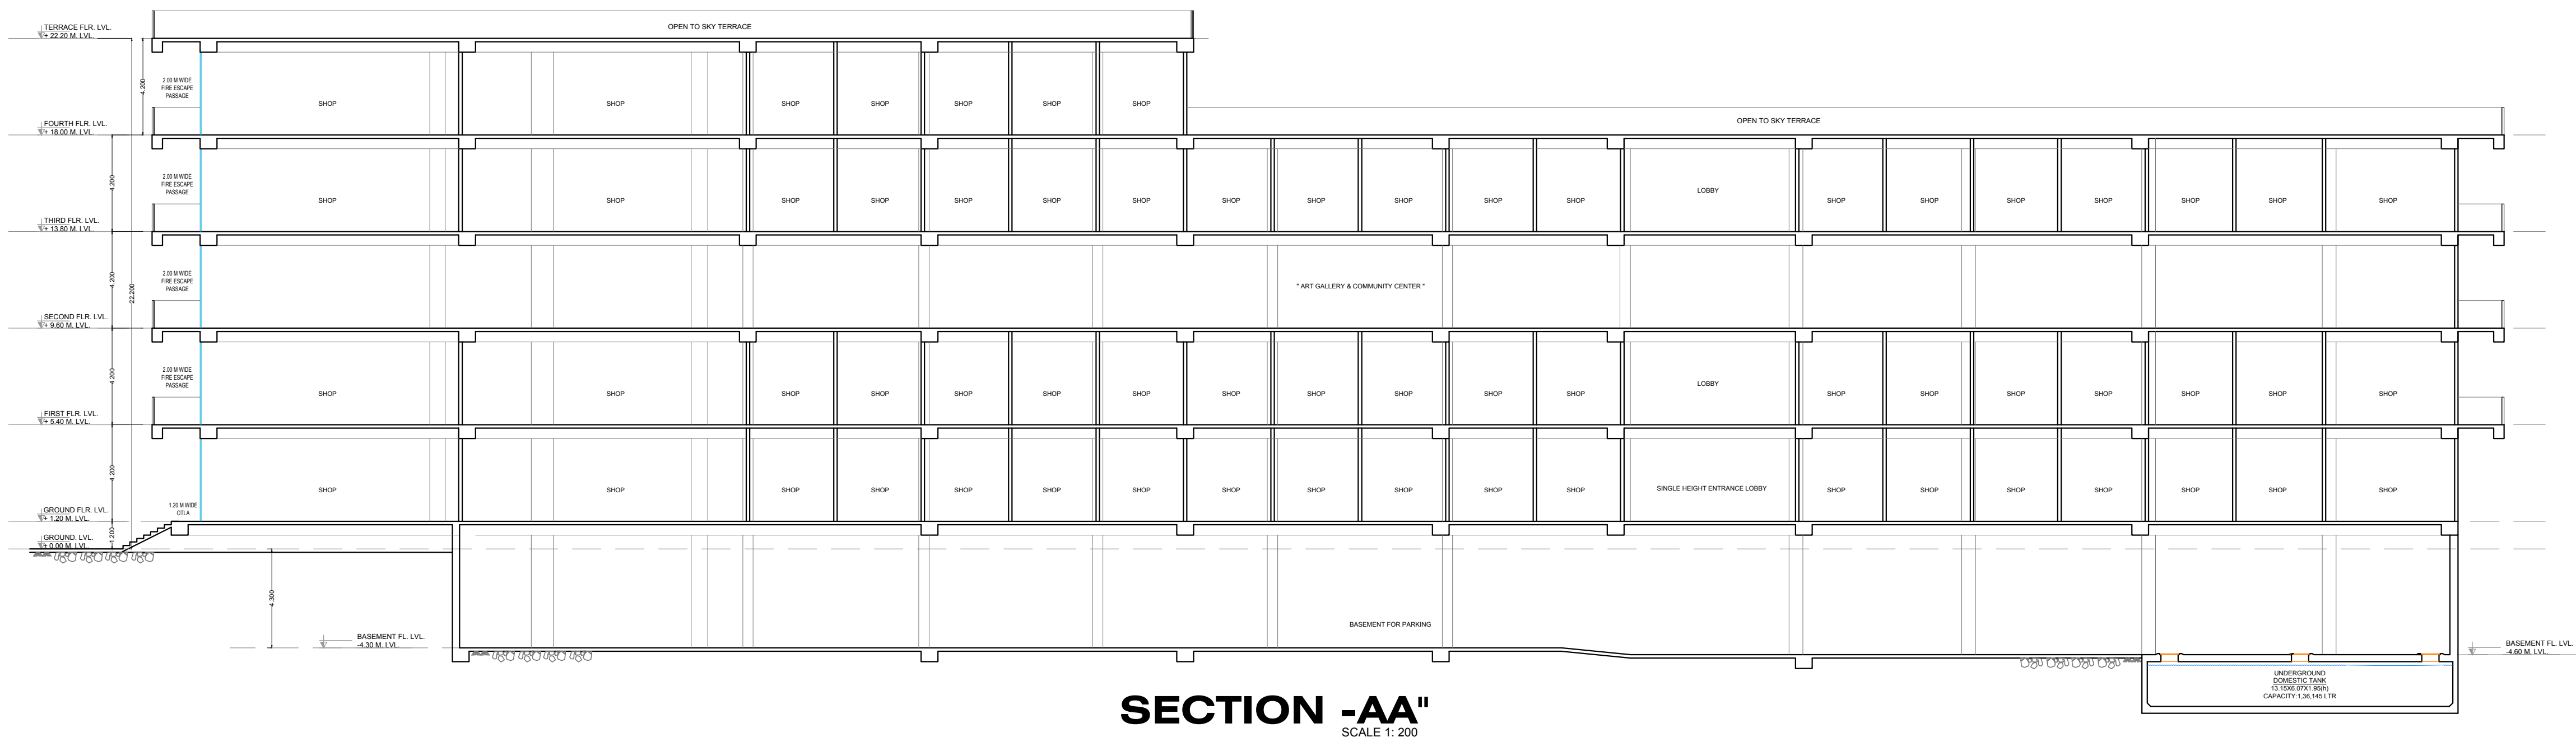

PROJECT PROPOSED FBT/BOT PROJECT OF "ART GALLERY & COMMUNITY CENTER" AND "COMMERCIAL COMPLEX" KNOWN AS "GANESHA GALAXY" ON RESERVATION NO. 27 AT LAL CHOWKY, JUNCTION OF AGRA ROAD AND AADHARWADI ROAD, ON PLOT BEARING S. NO. 1/1 OF VILLAGE KALYAN, TALUKA KALYAN, KALYAN WEST, THANE - 421301. PREVIOUS APPROVAL NO.: KDMC/NRV/BP/KV/2013-14/182 DATED: 24/2/2014 KALYAN DOMBIVLI MUNICIPAL CORPORATION


ARCHITECT



AR. ATIT MISTRY

ENVIRONMENTAL ARCHITECT + INTERIOR DESIGNER
info.aratitmistry@gmail.com

217, SHREE KRISHNA INDUSTRIAL PREMISES CSL, WESTERN EXPRESS HIGHWAY, DAHISAR EAST, MUMBAI, INDIA 400068

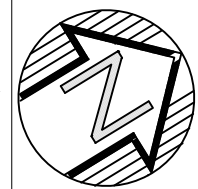

OWNER'S SIGN
FOR KDMC, THE CITY ENGINEER

CONCESSIONAIRE'S SIGN
FOR DHANSHREE DEVELOPERS PVT. LTD.

ARCHITECT'S SIGN