

PARTICULARS	BUILT-UP AREA STATEMENT				ART GALLERY			
	NET BUA	80% ANCILLARY AREA	TOTAL BUA (A)	NET BUA	80% ANCILLARY AREA	TOTAL BUA (B)	TOTAL BUA (A+B)	
GRD FLOOR	2193.66	531.42	2725.08	418.47	294.17	712.65	3437.73	
1ST FLOOR	2564.27	2466.51	3812.78	0.00	0.00	0.00	3812.78	
2ND FLOOR	0.00	0.00	0.00	2218.85	1593.93	3812.78	3812.78	
3RD FLOOR	0.00	0.00	0.00	2218.85	1593.93	3812.78	3812.78	
4TH FLOOR	1811.56	868.70	2680.26	1132.53	0.00	1132.53	3812.78	
5TH FLOOR	2627.67	1185.11	3812.78	0.00	0.00	0.00	3812.78	
6TH FLOOR	2627.67	1185.11	3812.78	0.00	0.00	0.00	3812.78	
7TH FLOOR	1159.39	938.47	2097.86	0.00	0.00	0.00	2097.86	
TOTAL PROPOSED	12984.22	5957.52	18941.55	5988.70	3482.03	9470.74	28412.28	
TOTAL PERMISSIBLE	10524.00	8419.20	18943.20	5262.00	4209.60	9471.60		
	-2460.22	2461.88	1.65	-726.70	727.57	0.86		

PARKING CALCULATIONS FOR "COMMERCIAL COMPLEX"			
Shops			
2 No. of Car Parking Spaces Required for every 100 sq. m.	6 No. of Scooter Parking Space Required for every 100 sq. m.		
261	783		
Multiplying Factor 0.8	Multiplying Factor 0.8		
209	626		
PARKING CALCULATIONS FOR "ART GALLERY & COMMUNITY CENTRE"			
Art Gallery & Community Centre			
1 No. of Car Parking Spaces Required for every 200 sq. m.	5 No. of Scooter Parking Space Required for every 200 sq. m.		
30	150		
Multiplying Factor 0.8	Multiplying Factor 0.8		
24	120		

SUMMARY OF PARKING STATEMENT		
Particulars	Car Parking Spaces	Scooter Parking Spaces
Total Required	233	746
Total Proposed	217	310
Net Difference	16	436
Total Parking Proposed	217	310



TOTAL CAR PARKING: 217
TOTAL SCOOTER PARKING: 180

BASEMENT PLAN

SCALE 1: 200

PROFORMA - A				
No	AREA STATEMENT	AREA IN SQ.MT.		
1	Plot Area	5262.00		
	(a) As per ownership document (7/12 extract)	5262.00		
	(b) as per measurement sheet	5262.00		
	(c) as per site	5262.00		
	(d) Total Plot Area considered for BUA calculations	5262.00		
2	Deductions for	---		
	(a) 5.00m wide DP road	NIL		
	(b) 24.00m wide DP road	NIL		
	(c) Total Deductions	---		
3	Balance area of plot (1-2)	5262.00		
4	Amenity Space (if applicable)	---		
	(a) Required (2% x ar. no. 3)	NIL		
	(b) Adjustment of 20% & 20% if any	NIL		
	(c) Balance Proposed	NIL		
5	Net Plot Area (1+4)	5262.00		
6	Recreational Open Space (if applicable)	---		
	(a) Required (10% x ar. no. 3)	NIL		
	(b) Proposed	NIL		
7	Internal Road area	NIL		
8	Portable area (if applicable)	5262.00		
PARTICULARS		1/3rd AREA FOR "COMM. GALLERY & COMMUNITY CENTER"	2/3rd AREA FOR "CONCESSIONARY COMMERCIAL COMPLEX"	TOTAL
9	Built up area as per reg. no. 7.1, table 7.1.A, point no. E (Sr. No. 5 x 3.00)	5262.00	10524.00	15786.00
10	Addition of FSI on payment of premium	NIL	NIL	NIL
	(a) Maximum permissible premium FSI - based on road width / TGD Zone. (540.00)	NIL	NIL	NIL
	(b) Proposed premium FSI	NIL	NIL	NIL
11	In-situ FSI / TOR loading	NIL	NIL	NIL
	(a) In-situ area DP Road (2.00x24.00)	NIL	NIL	NIL
	(b) In-situ area against Amenity Space if handed over (2.00 x 1.85 x 4b and / or 4c))	NIL	NIL	NIL
	(c) TOR area permissible (540.00)	NIL	NIL	NIL
	(d) Total in-situ FSI / TOR loading proposed	NIL	NIL	NIL
12	Additional FSI area under Chapter No. 7	NIL	NIL	NIL
13	Total entitlement of FSI in the proposal	5262.00	10524.00	15786.00
	(a) If > 100% (100% or 10% whichever is applicable)	4209.60	8419.20	12628.80
	(b) Ancillary area up to 80% with payment of charges	8471.60	16943.20	25414.80
	(c) Total Entitlement (a+b)	12681.20	25362.40	38043.60
14	Max. utilization of FSI (building potential) as per road width (as per reg. no. 6.1 or 6.2 or 6.3 or 6.4 as applicable) x 1.8	12681.20	18943.20	31624.40
15	Total Built-up Area in proposal (including area at Sr.No.17.3)	NIL	130.00	130.00
	(a) Existing Built-up Area of Mandir	NIL	130.00	130.00
	(b) Proposed Built-up Area (as per P-Form)	8471.60	16813.20	25284.80
	(c) Total Built-up Area (a+b)	8471.60	16943.20	25414.80
16	FSI Consumed (10%) (should not be more than sr. no. 15)	NIL	5.40	5.40
17	Area for inclusive Housing, if any	NIL	NIL	NIL
	(a) Required (20% of Sr.No.5)	NIL	NIL	NIL
	(b) Proposed	NIL	NIL	NIL
18	Balance BUA including ancillary area	NIL	NIL	NIL

CERTIFIED THAT THE PLOT UNDER REFERENCE WAS SURVEYED BY ME ON 15/03/11 & THE DIMENSIONS OF SIDES ETC. OF PLOT STATED ON PLAN ARE AS MEASURED ON THE SITE & THE AREA SO WORKED OUT TALLIES WITH THE AREA STATED IN THE DOCUMENT OF OWNERSHIP/7.12. SCHEME RECORDS/DEPTT./CITY SURVEY RECORDS.

PROPOSED FBT/BOT PROJECT OF "ART GALLERY & COMMUNITY CENTER" AND "COMMERCIAL COMPLEX" KNOWN AS "GANESHA GALAXY" ON RESERVATION NO. 27 AT LAL CHOWKY, JUNCTION OF AGRA ROAD AND AADHARWADI ROAD, ON PLOT BEARING S. NO. 1/1 OF VILLAGE KALYAN, TALUKA KALYAN, KALYAN WEST, THANE - 421301. PREVIOUS APPROVAL NO. KMC/NR/SPR/2013-14/182 DATED 24/2/2014 KALYAN DOMBIVLI MUNICIPAL CORPORATION

ARCHITECT
Ar. ATIT MISTRY
ENVIRONMENTAL ARCHITECT + INTERIOR DESIGNER
info.aratimistry@gmail.com
217, SHREE KRISHNA INDUSTRIAL PREMISES CSL, WESTERN EXPRESS HIGHWAY, DAHISAR EAST, MUMBAI, INDIA 400068

OWNER'S SIGN
FOR KMC, THE CITY ENGINEER

CONCESSIONAIRE'S SIGN
FOR SHANESHA DEVELOPERS PVT. LTD.

ARCHITECT'S SIGN




OWNER'S SIGN
FOR KDMC, THE CITY ENGINEER

CONCESSIONAIRE'S SIGN
FOR DHANSHREE DEVELOPERS PVT. LTD.

ARCHITECT'S SIGN

ARCHITECT

▲ A. B. ATIT MISTD

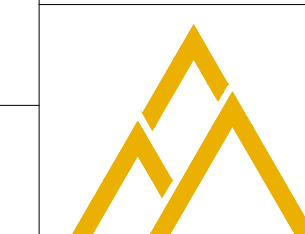


AR. ATIT MISTRY

ENVIRONMENTAL ARCHITECT + INTERIOR DESIGNER
info.aratitmistry@gmail.com

217, SHREE KRISHNA INDUSTRIAL PREMISES CSL, WESTERN EXPRESS HIGHWAY, DAHISAR EAST, MUMBAI, INDIA 400068



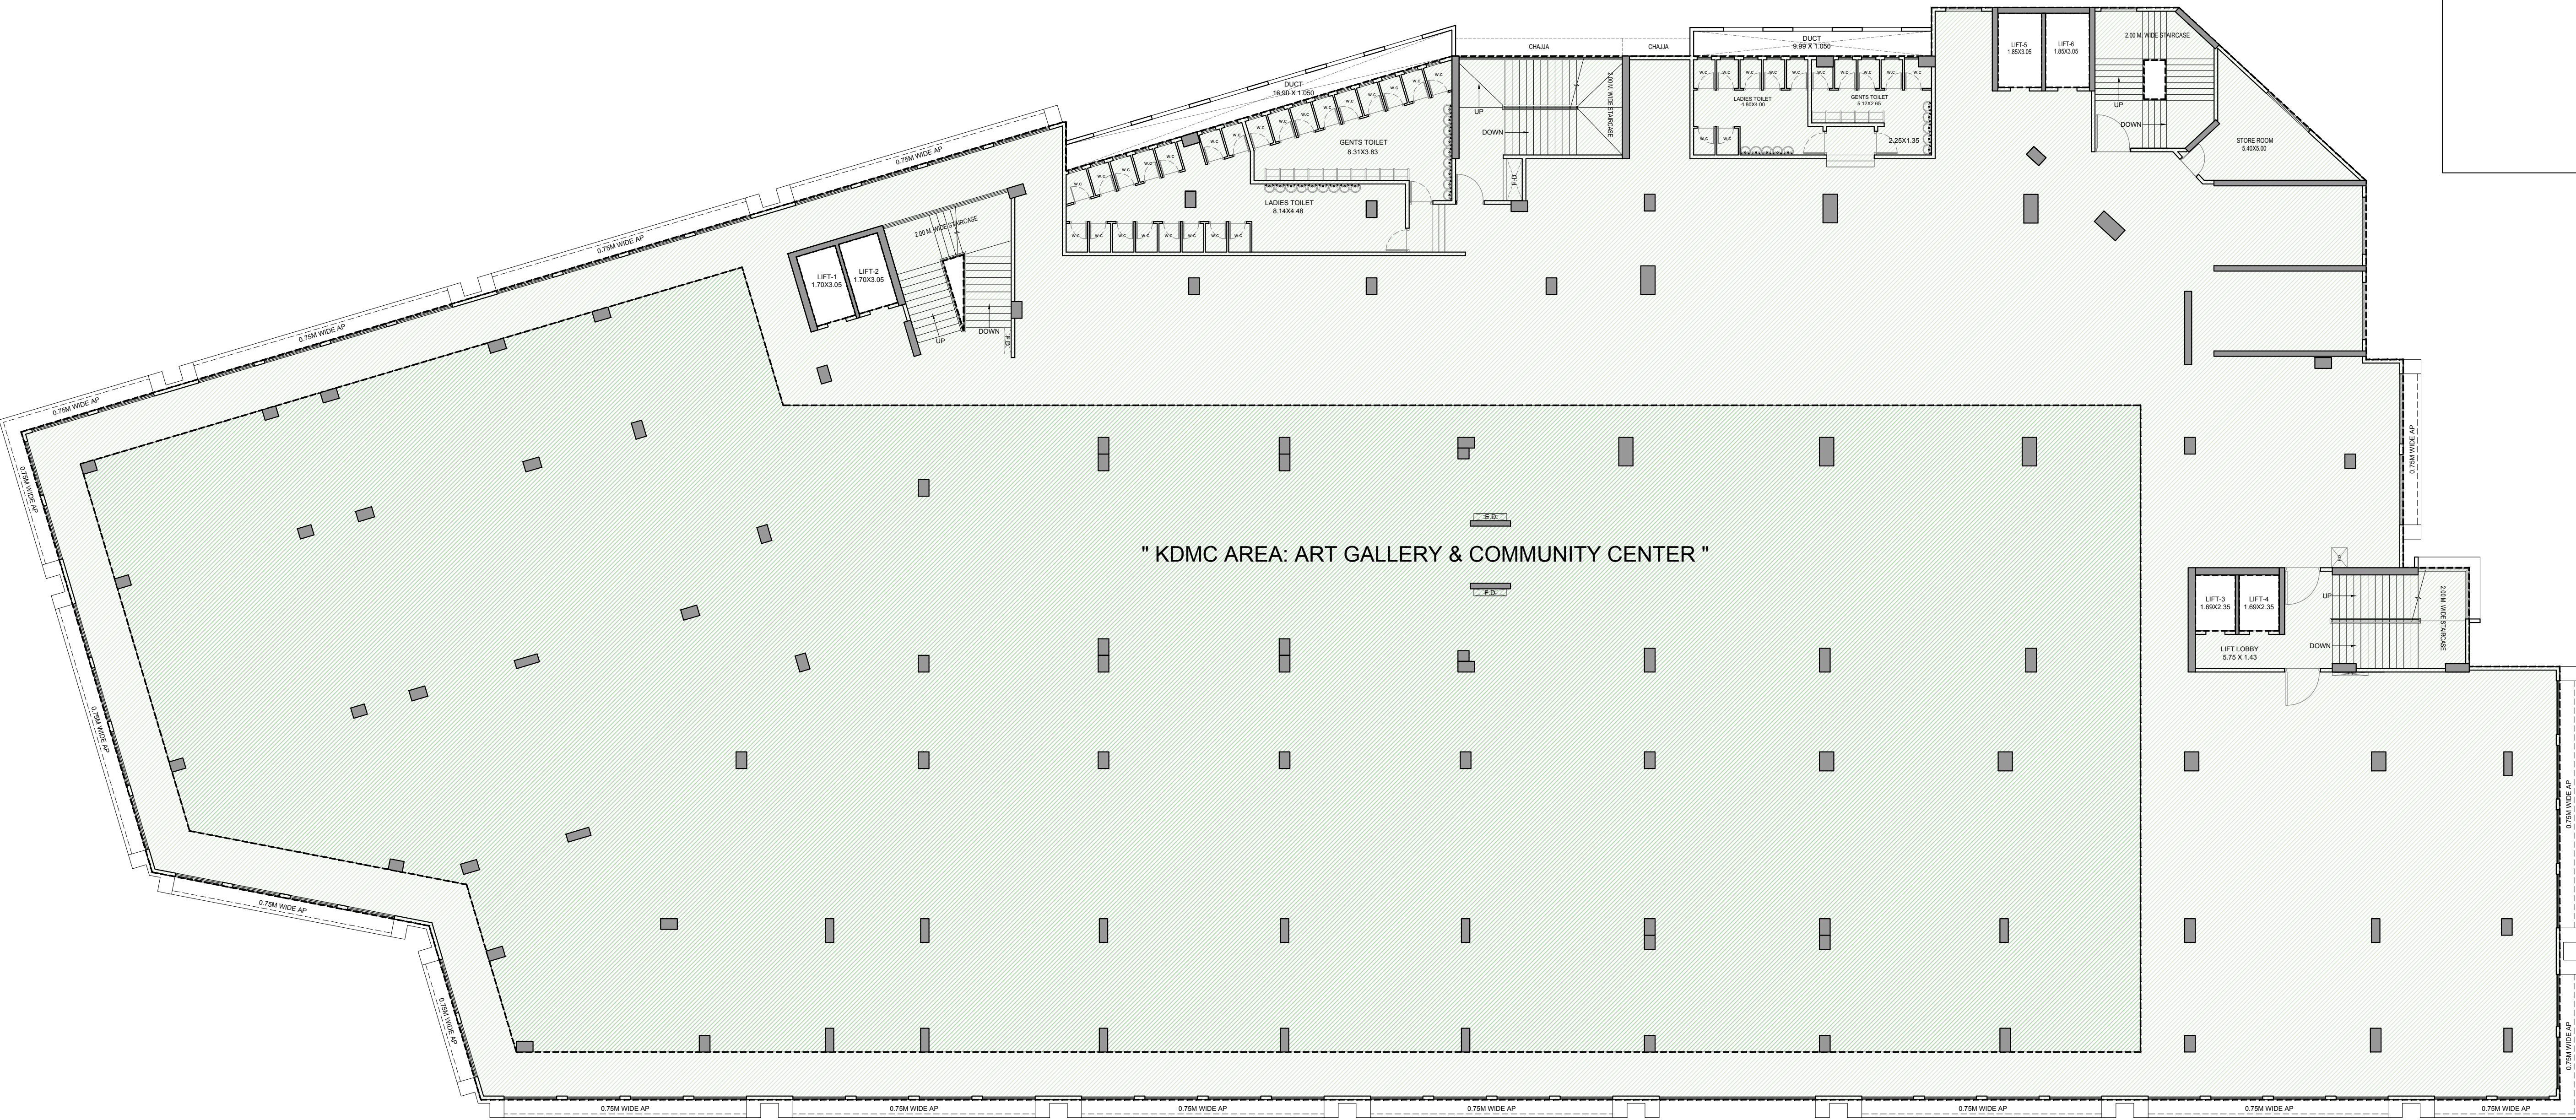

2ND & 3RD FLOOR PLAN


SCALE 1: 100

PROJECT PROPOSED FBT/BOT PROJECT OF "ART GALLERY & COMMUNITY CENTER" AND "COMMERCIAL COMPLEX" KNOWN AS "GANESHA GALAXY" ON RESERVATION NO. 27 AT LAL CHOWKY, JUNCTION OF AGRA ROAD AND AADHARWADI ROAD, ON PLOT BEARING S. NO. 1/1 OF VILLAGE KALYAN, TALUKA KALYAN, KALYAN WEST, THANE - 421301. PREVIOUS APPROVAL NO. KDMC/NR/BR/KV/2013-14/182 DATED 24/2/2014. KALYAN DOMBIVLI MUNICIPAL CORPORATION.


ARCHITECT



Ar. ATIT MISTRY
ENVIRONMENTAL ARCHITECT + INTERIOR DESIGNER
info.aratimistry@gmail.com
217, SHREE KRISHNA INDUSTRIAL PREMISES CSL, WESTERN EXPRESS HIGHWAY, DAHSAR EAST, MUMBAI, INDIA 400068

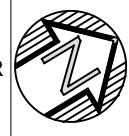

OWNER'S SIGN FOR KDMC, THE CITY ENGINEER	CONCESSIONAIRE'S SIGN FOR DHANSHREE DEVELOPERS PVT. LTD.	ARCHITECT'S SIGN
---	---	------------------

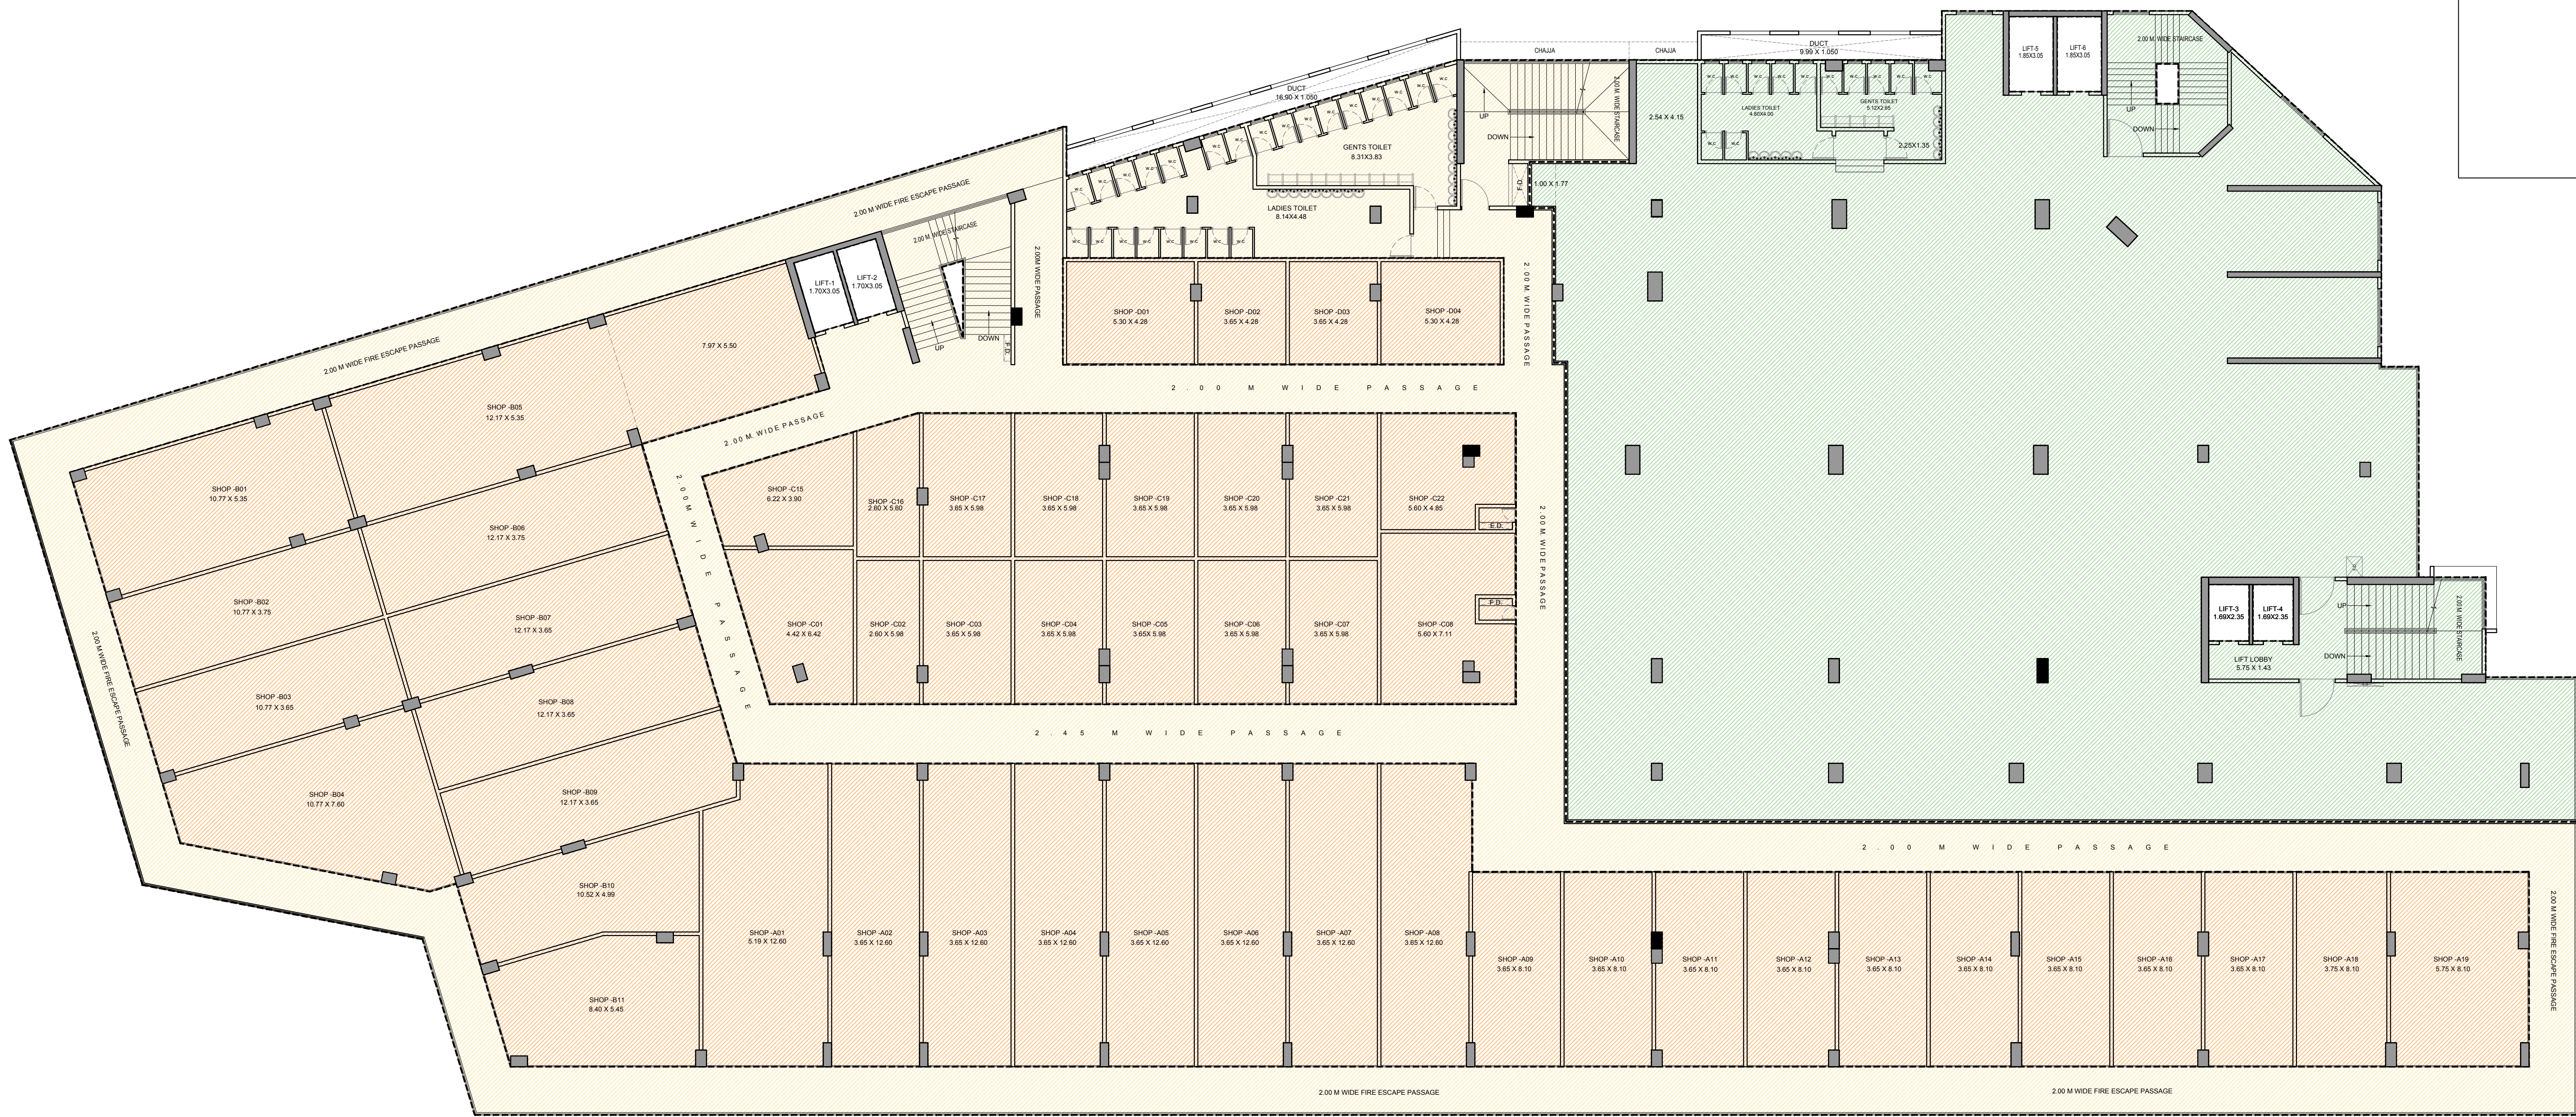

4TH FLOOR PLAN
SCALE 1: 100

PROPOSED FBT/BOT PROJECT OF "ART GALLERY & COMMUNITY CENTER" AND "COMMERCIAL COMPLEX" KNOWN AS "GANESHA GALAXY" ON RESERVATION NO. 27 AT LAL CHOWKY, JUNCTION OF AGRA ROAD AND AADHARWADI ROAD, ON PLOT BEARING S. NO. 1/11 OF VILLAGE KALYAN, TALUKA KALYAN, KALYAN WEST, THANE - 421301
PREVIOUS APPROVAL NO. KDMC/NR/BB/KV/2013-14/182 DATED 24/2/2014
KALYAN DOMBIVLI MUNICIPAL CORPORATION

ARCHITECT



Ar. ATIT MISTRY


ENVIRONMENTAL ARCHITECT + INTERIOR DESIGNER
info.aratimistry@gmail.com
217, SHREE KRISHNA INDUSTRIAL PREMISES CSL, WESTERN EXPRESS HIGHWAY, DAHSAR EAST, MUMBAI, INDIA 400068



OWNER'S SIGN
FOR KDMC, THE CITY ENGINEER

CONCESSIONAIRE'S SIGN
FOR DHANSHREE DEVELOPERS PVT. LTD.

ARCHITECT'S SIGN

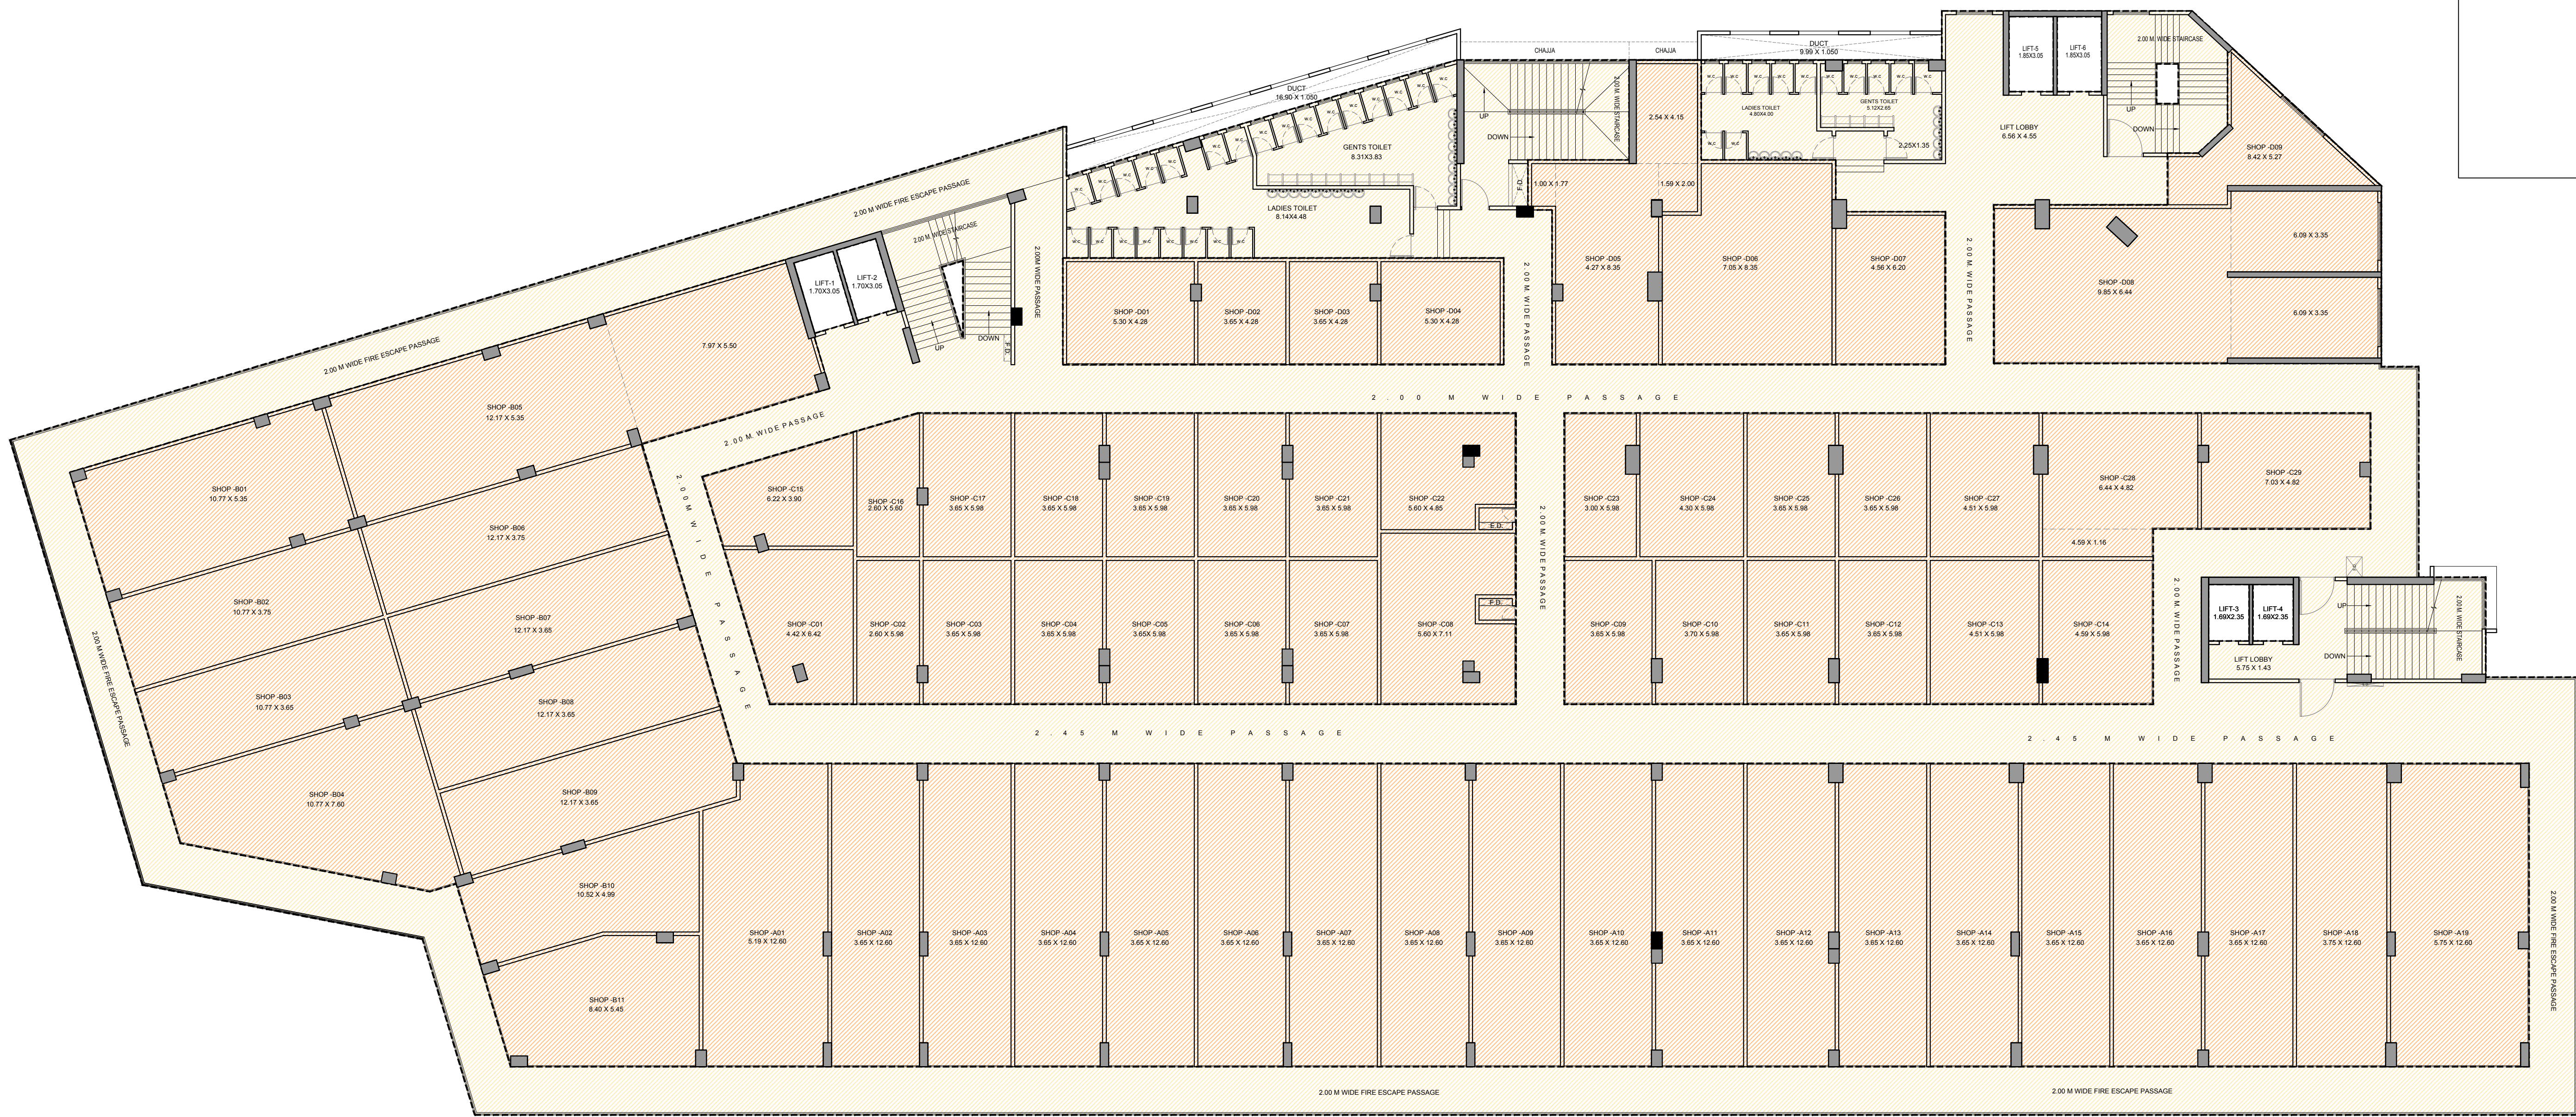

5TH & 6TH FLOOR PLAN

SCALE 1: 100

PROPOSED FBT/BOT PROJECT OF "ART GALLERY & COMMUNITY CENTER" AND "COMMERCIAL COMPLEX" KNOWN AS "GANESHA GALAXY" ON RESERVATION NO. 27 AT LAL CHOWKY, JUNCTION OF AGRA ROAD AND AADHARWADI ROAD, ON PLOT BEARING S. NO. 1/1 OF VILLAGE KALYAN, TALUKA KALYAN, KALYAN WEST, THANE - 421301. PREVIOUS APPROVAL NO. KDMC/CR/BI/PC/2013-14/182 DATED 24/2/2014. KALYAN DOMBIVLI MUNICIPAL CORPORATION.

ARCHITECT



Ar. ATIT MISTRY


ENVIRONMENTAL ARCHITECT + INTERIOR DESIGNER
info.aratimistry@gmail.com
217, SHREE KRISHNA INDUSTRIAL PREMISES CSL, WESTERN EXPRESS HIGHWAY, DAHSAR EAST, MUMBAI, INDIA 400068



OWNER'S SIGN
FOR DMDC, THE CITY ENGINEER

CONCESSIONAIRE'S SIGN
FOR DHANSHREE DEVELOPERS PVT. LTD.

ARCHITECT'S SIGN

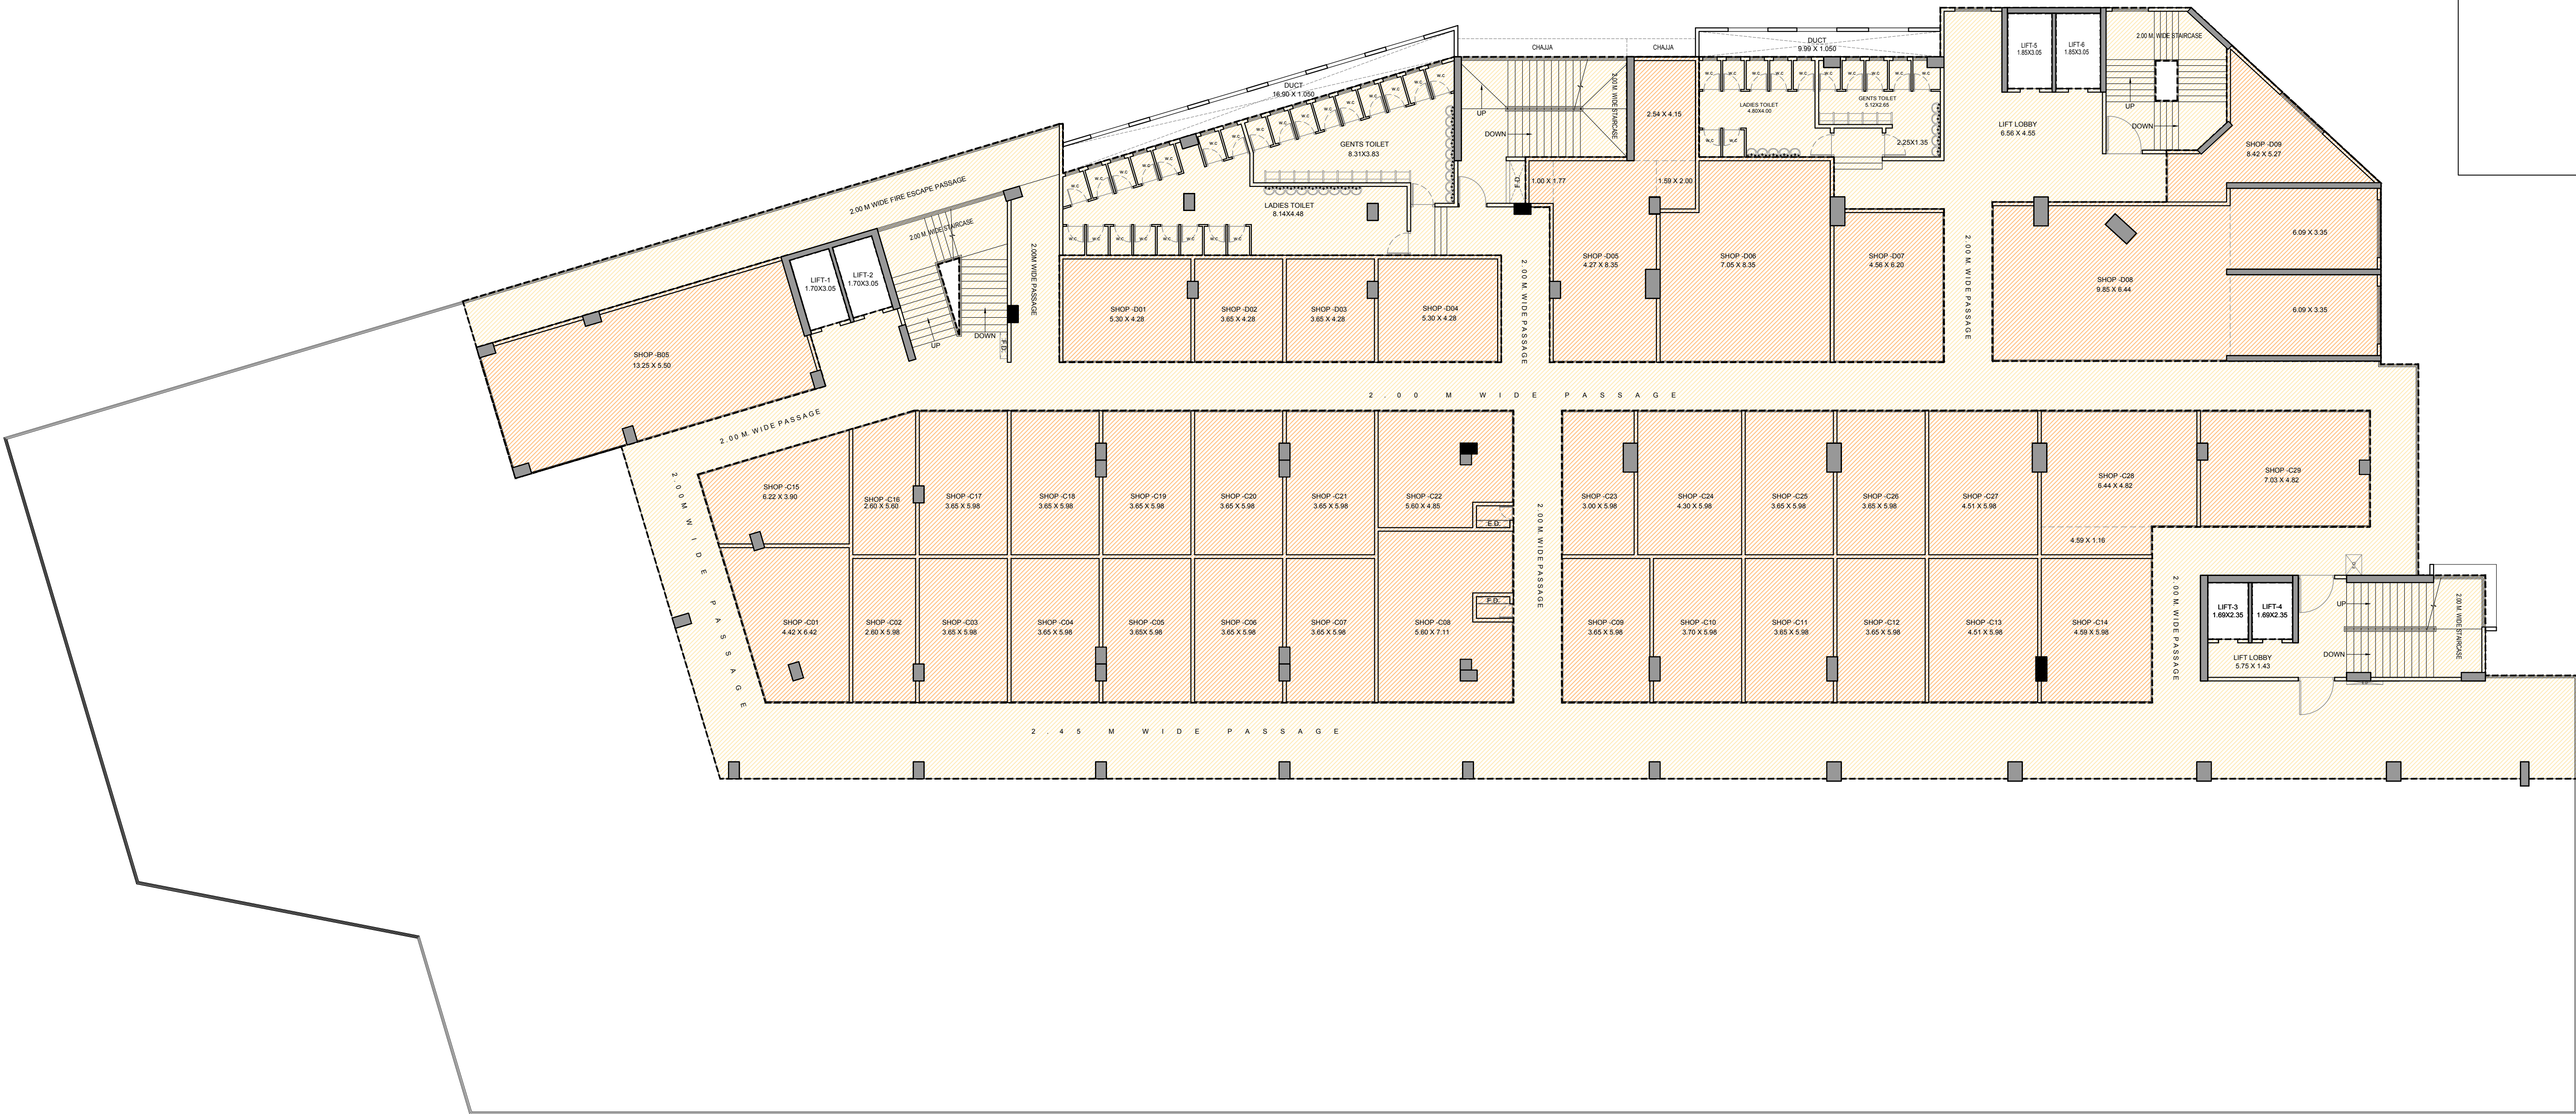

7TH FLOOR PLAN
SCALE 1: 100

PROPOSED FBT/BOT PROJECT OF "ART GALLERY & COMMUNITY CENTER" AND "COMMERCIAL COMPLEX" KNOWN AS "GANESHA GALAXY" ON RESERVATION NO. 27 AT LAL CHOWKY, JUNCTION OF AGRA ROAD AND AADHARWADI ROAD, ON PLOT BEARING S. NO. 1/11 OF VILLAGE KALYAN, TALUKA KALYAN, KALYAN WEST, THANE - 421301. PREVIOUS APPROVAL NO. KDMC/NR/BJ/KV/2013-14/182 DATED 24/2/2014. KALYAN DOMBIVLI MUNICIPAL CORPORATION.

ARCHITECT



Ar. ATIT MISTRY


ENVIRONMENTAL ARCHITECT + INTERIOR DESIGNER
info.aratimistry@gmail.com
217, SHREE KRISHNA INDUSTRIAL PREMISES CSL, WESTERN EXPRESS HIGHWAY, DAHSAR EAST, MUMBAI, INDIA 400068




OWNER'S SIGN
FOR KDMC, THE CITY ENGINEER

CONCESSIONAIRE'S SIGN
FOR DHANSHREE DEVELOPERS PVT. LTD.


ARCHITECT'S SIGN

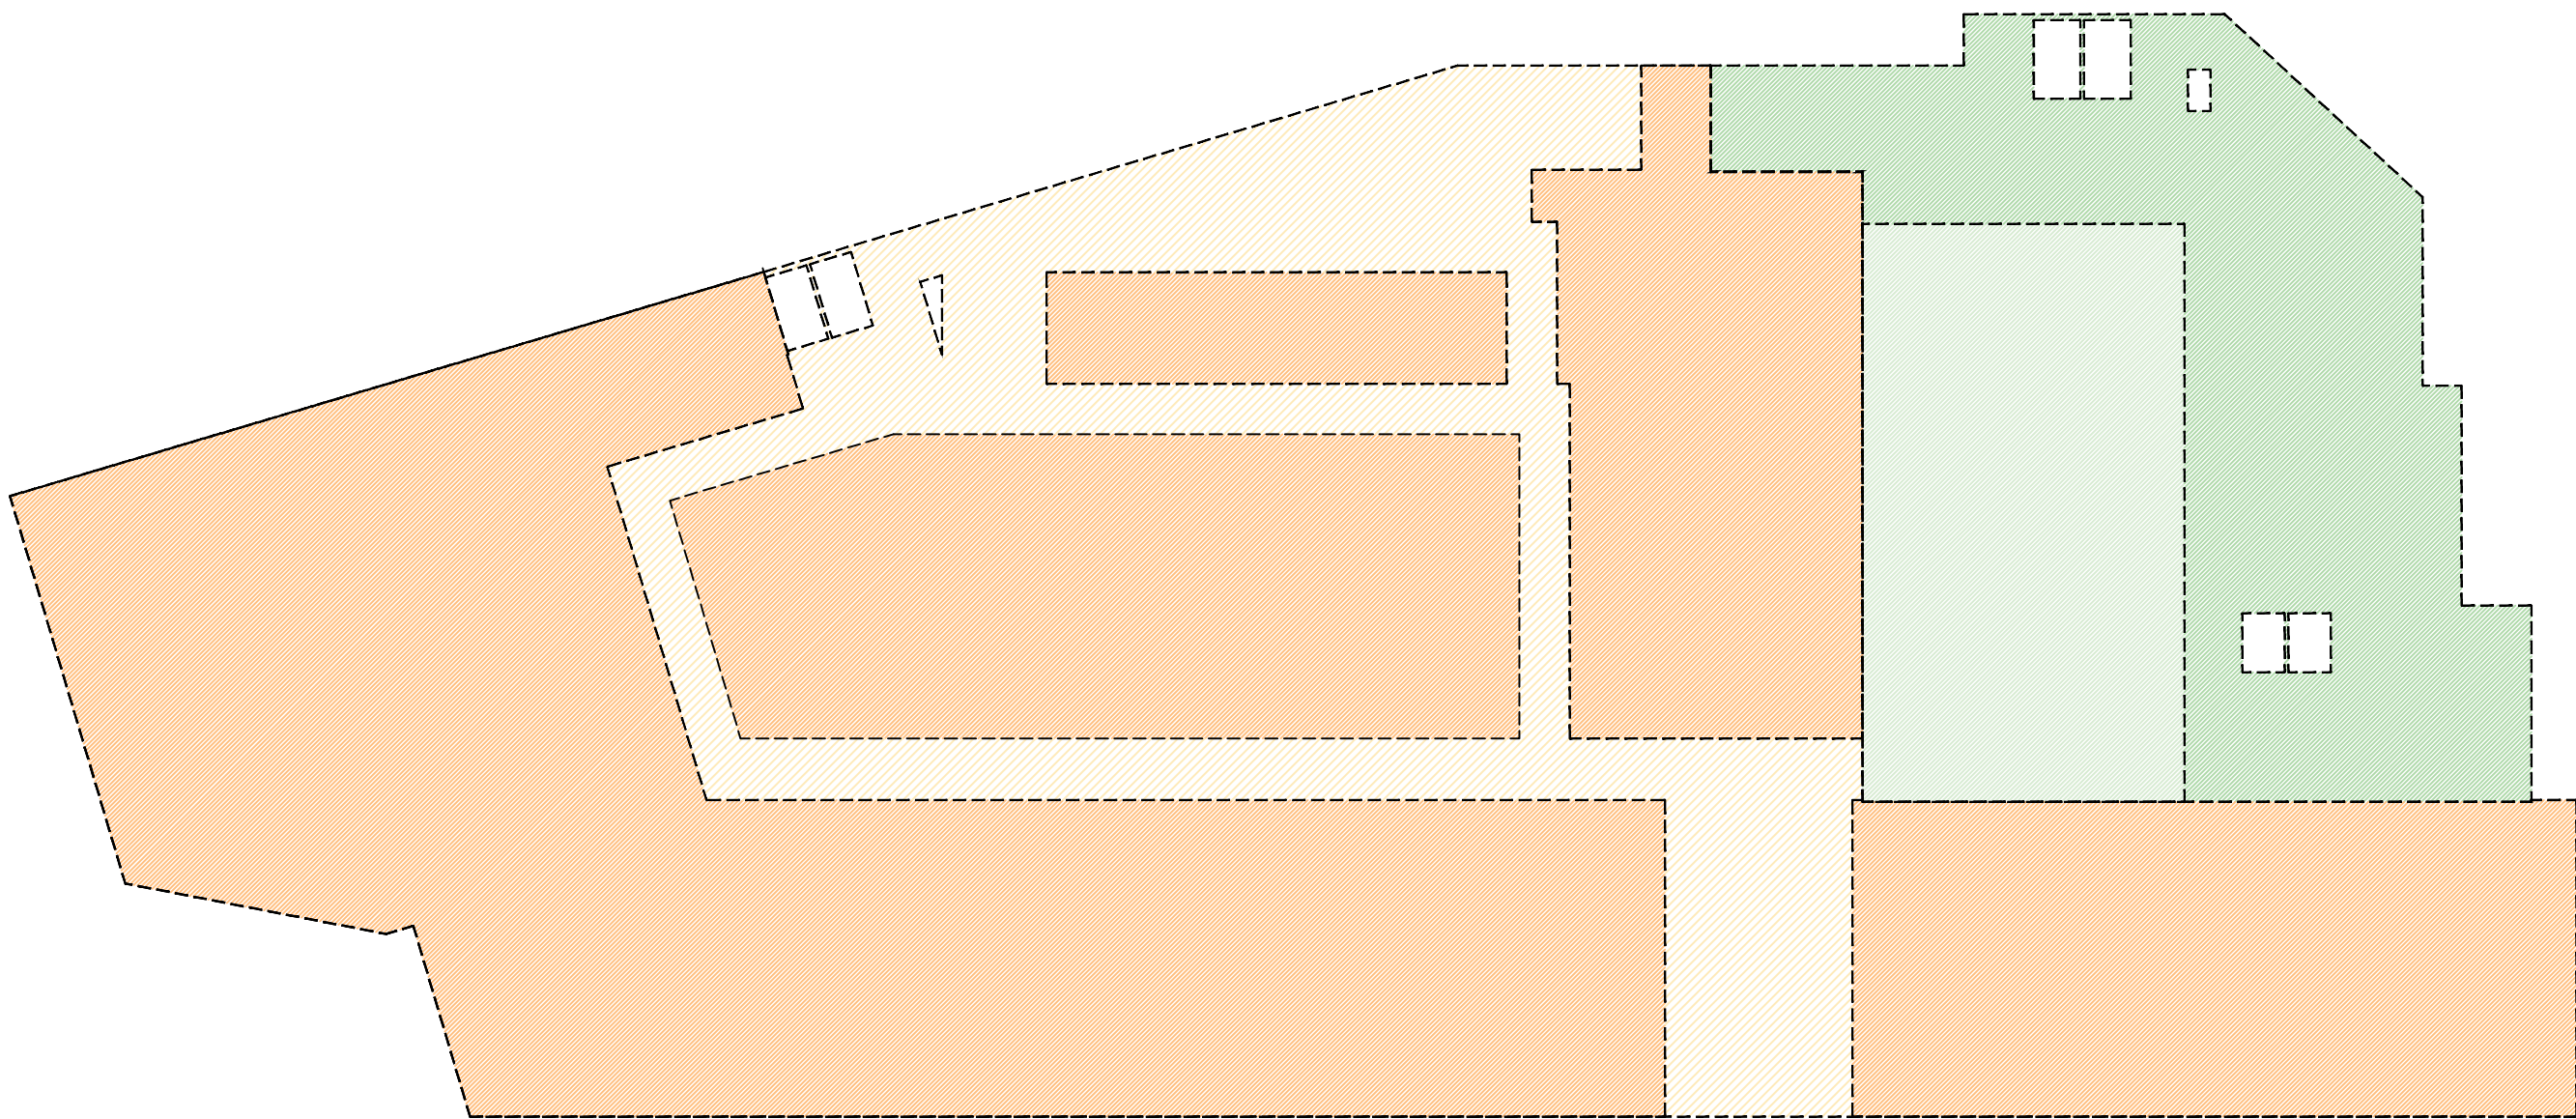


AREA CALCULATION & DIAGRAM FOR GROUND FLOOR
SCALE 1:200

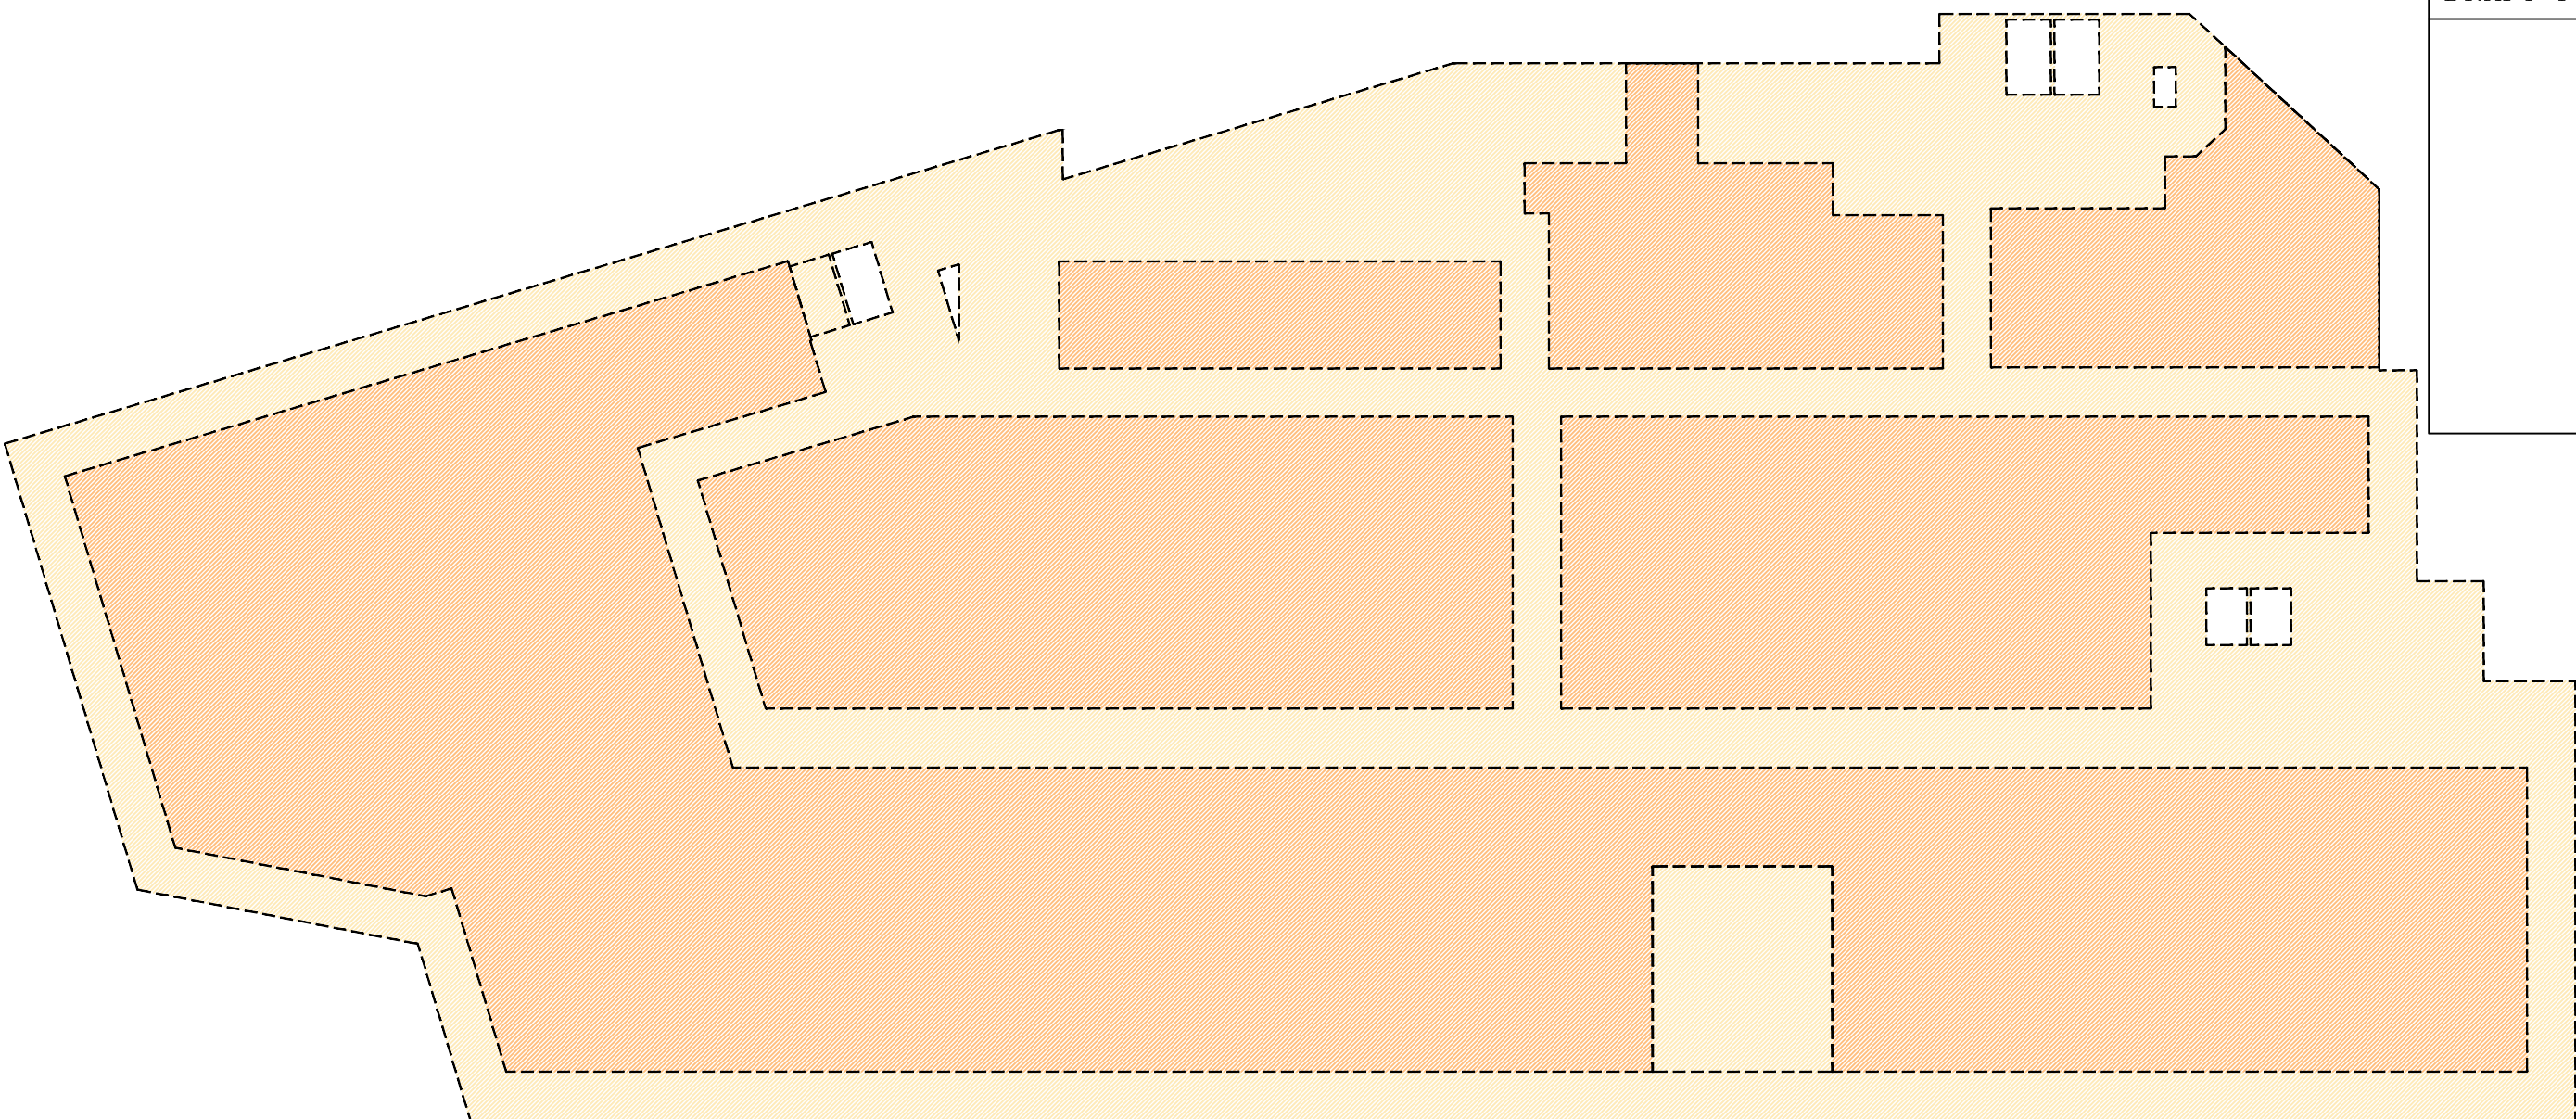


AREA CALCULATION & DIAGRAM FOR FIRST FLOOR
SCALE 1:200

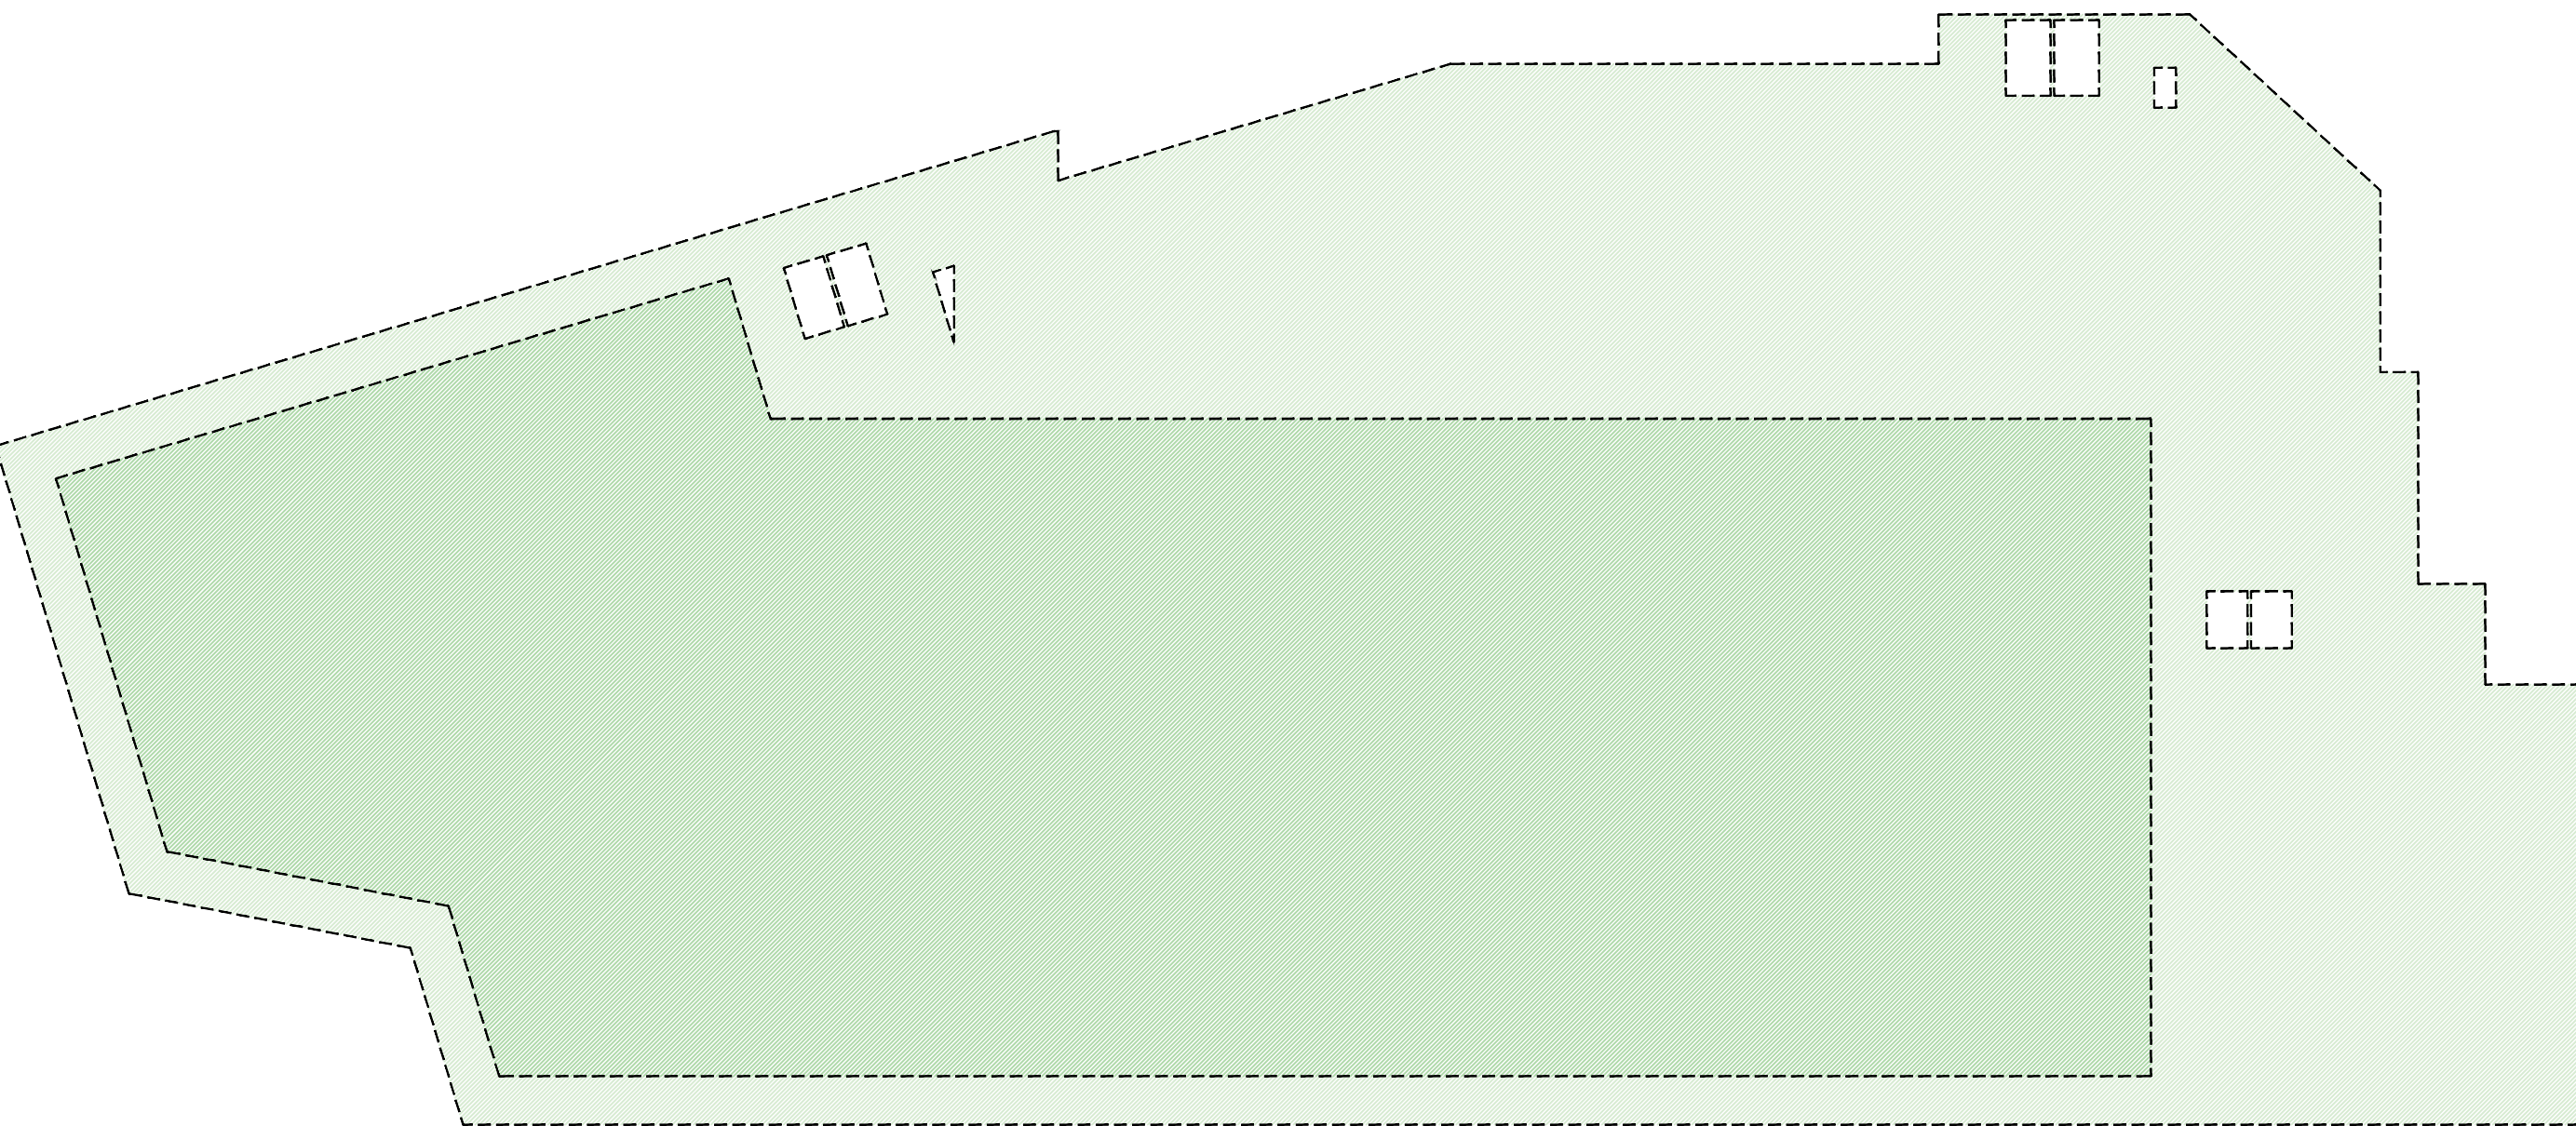

AREA CALCULATION & DIAGRAM FOR SECOND AND THIRD FLOOR
SCALE 1:200

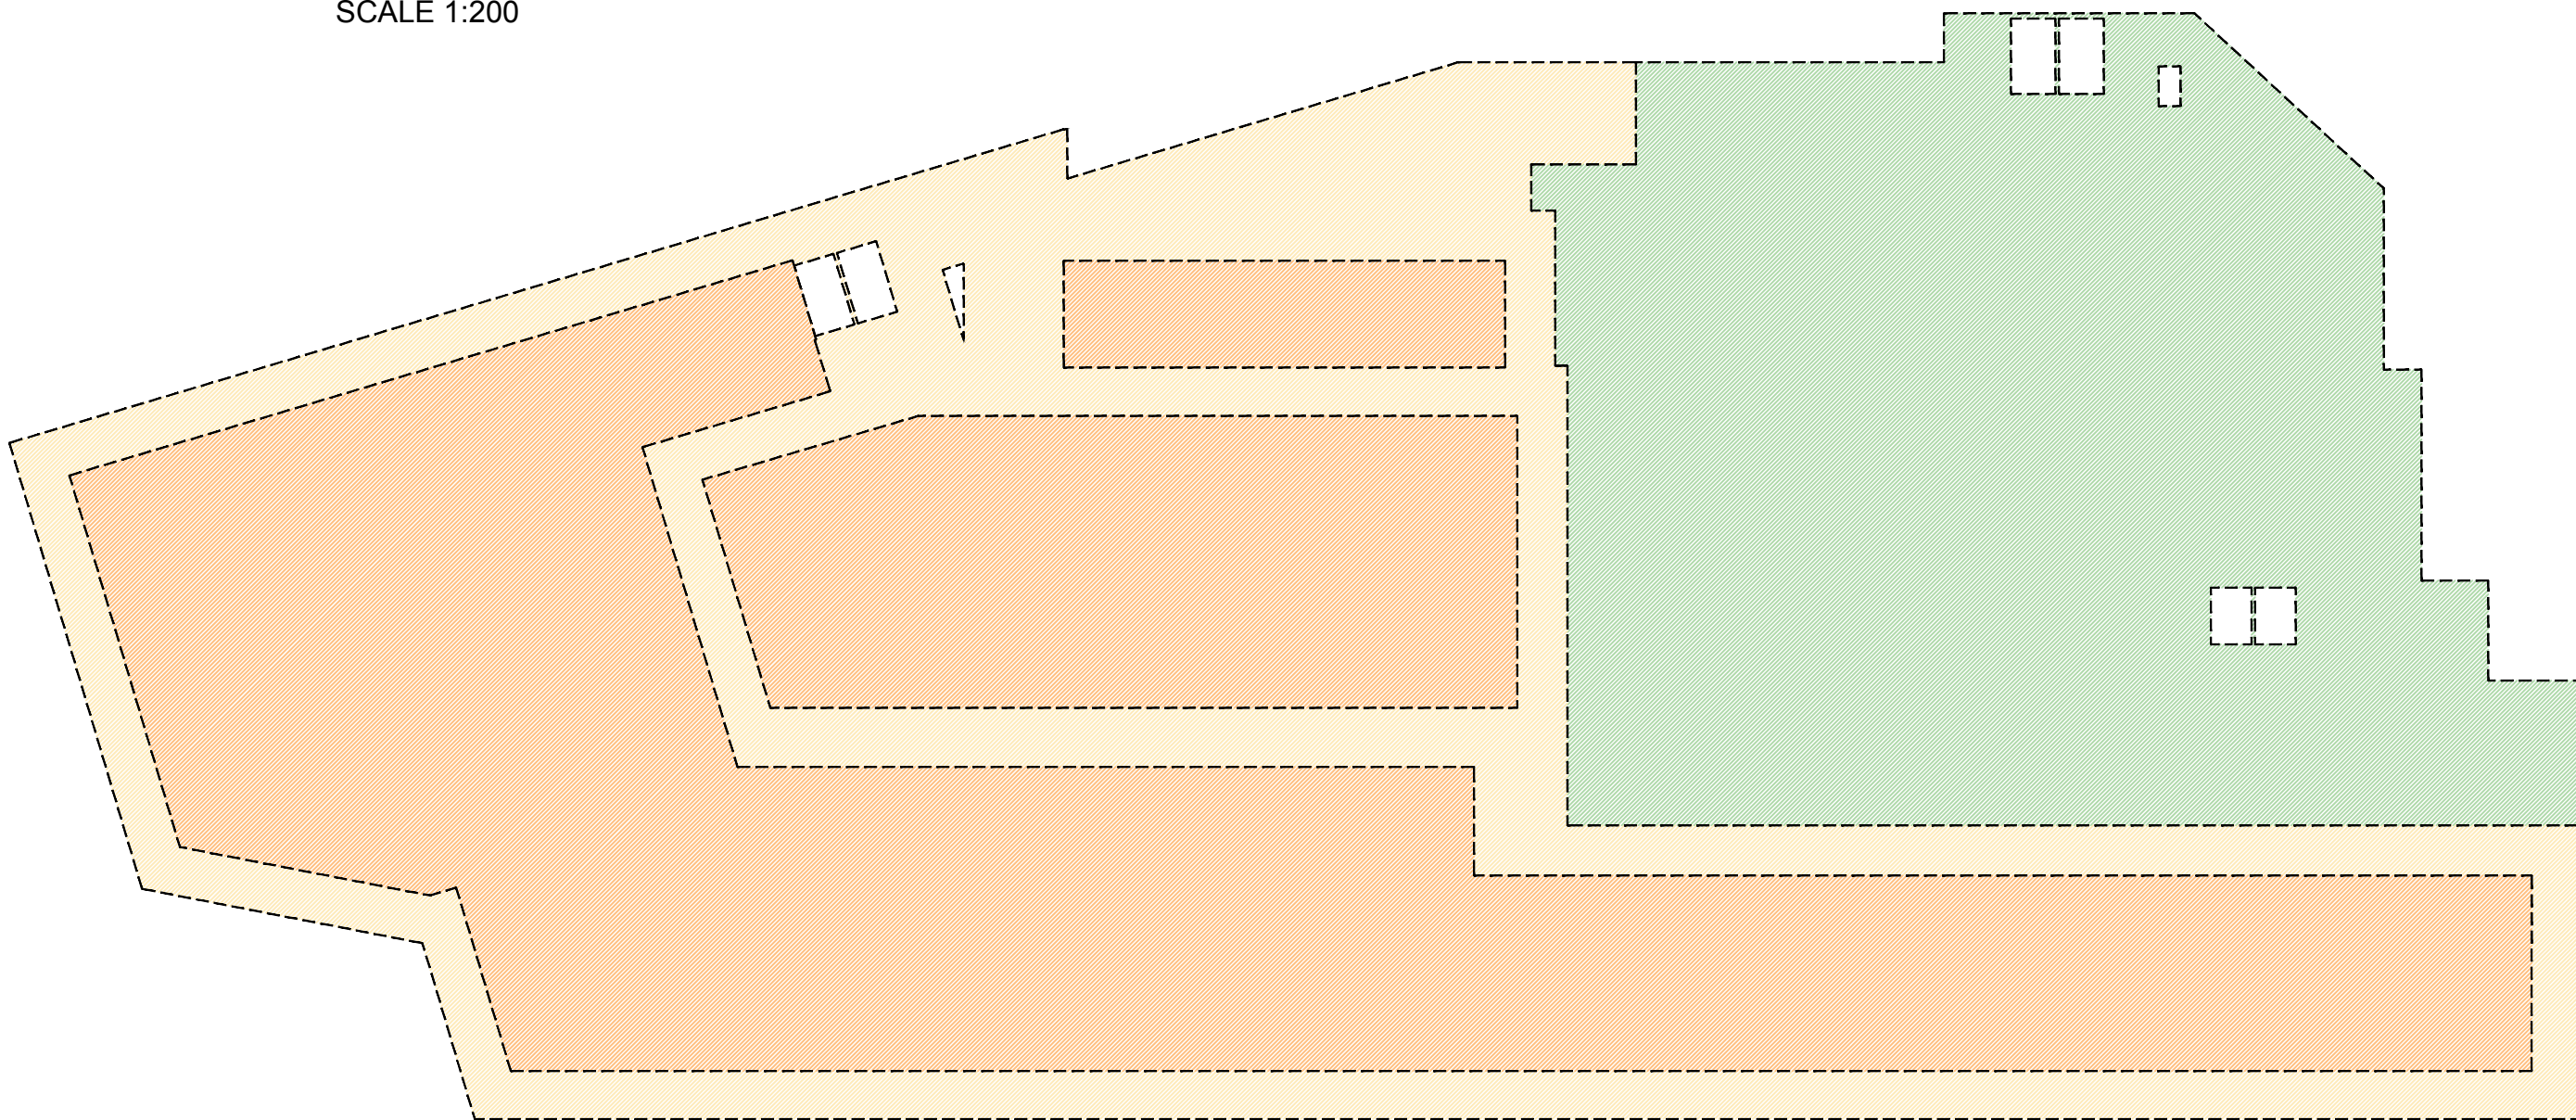


AREA CALCULATION & DIAGRAM FOR FOURTH FLOOR
SCALE 1:200

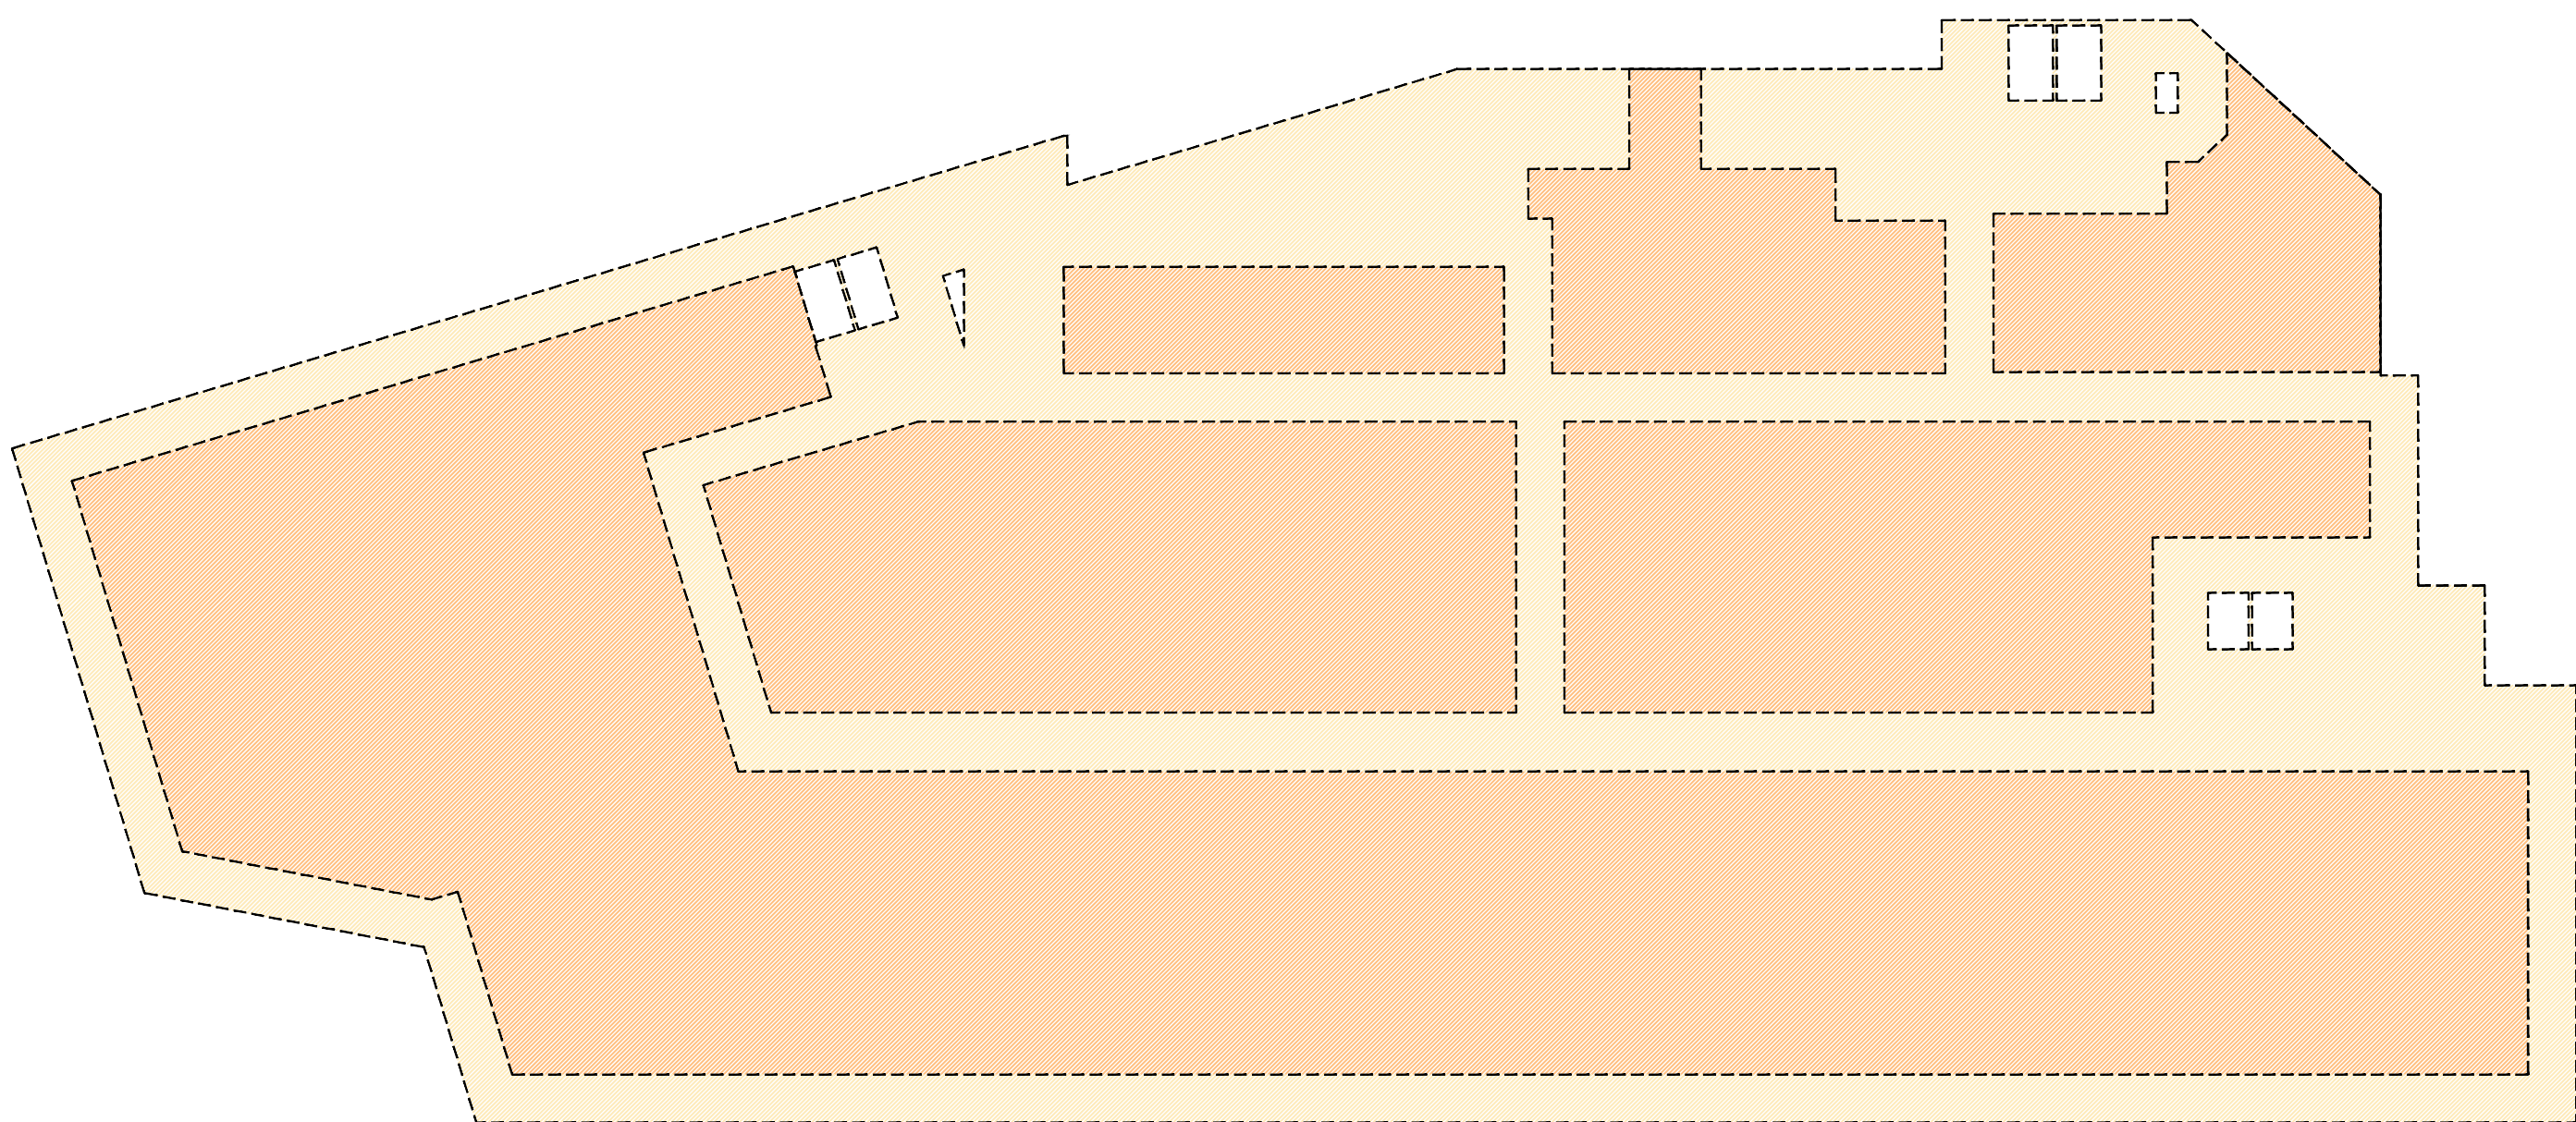

AREA CALCULATION & DIAGRAM FOR FIFTH AND SIXTH FLOOR

SCALE 1:200

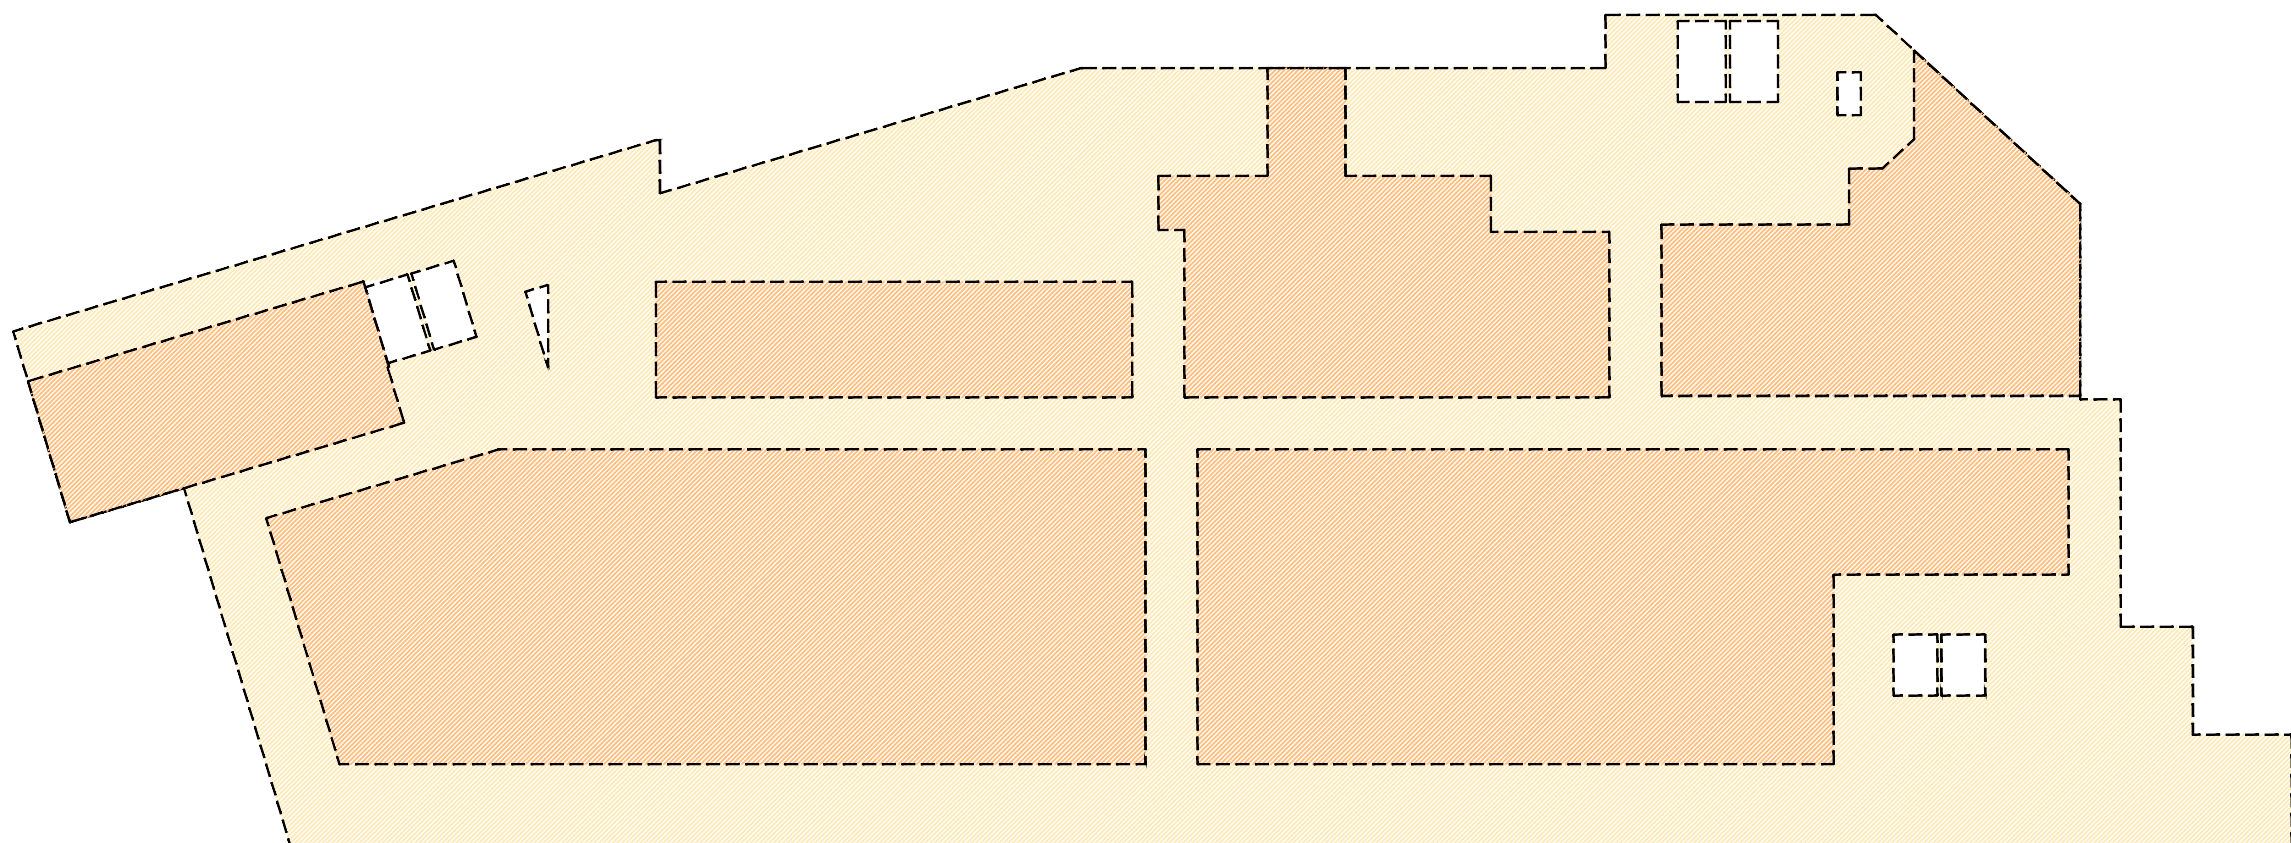

AREA CALCULATION & DIAGRAM FOR SEVENTH FLOOR

SCALE 1:200

PROJECT PROPOSED FBT/BOT PROJECT OF "ART GALLERY & COMMUNITY CENTER" AND "COMMERCIAL COMPLEX" KNOWN AS "GANESHA GALAXY" ON RESERVATION NO. 27 AT LAL CHOWKY, JUNCTION OF AGRA ROAD AND AADHARWADI ROAD, ON PLOT BEARING S. NO. 1/1 OF VILLAGE KALYAN, TALUKA KALYAN, KALYAN WEST, THANE - 421301 PREVIOUS APPROVAL NO. KDMCNRV/BPKV/2013-14/182 DATED 24/2/2014 KALYAN DOMBIVLI MUNICIPAL CORPORATION

ARCHITECT



Ar. ATIT MISTRY

ENVIRONMENTAL ARCHITECT + INTERIOR DESIGNER
info.aratimistry@gmail.com
217, SHREE KRISHNA INDUSTRIAL PREMISES CSL, WESTERN EXPRESS HIGHWAY, DAHSAR EAST, MUMBAI, INDIA 400068



OWNER'S SIGN
FOR KDMC, THE CITY ENGINEER

CONCESSIONAIRE'S SIGN
FOR DHANSHREE DEVELOPERS PVT. LTD.

ARCHITECT'S SIGN